

PLAN RDC — PROJET COTÉ

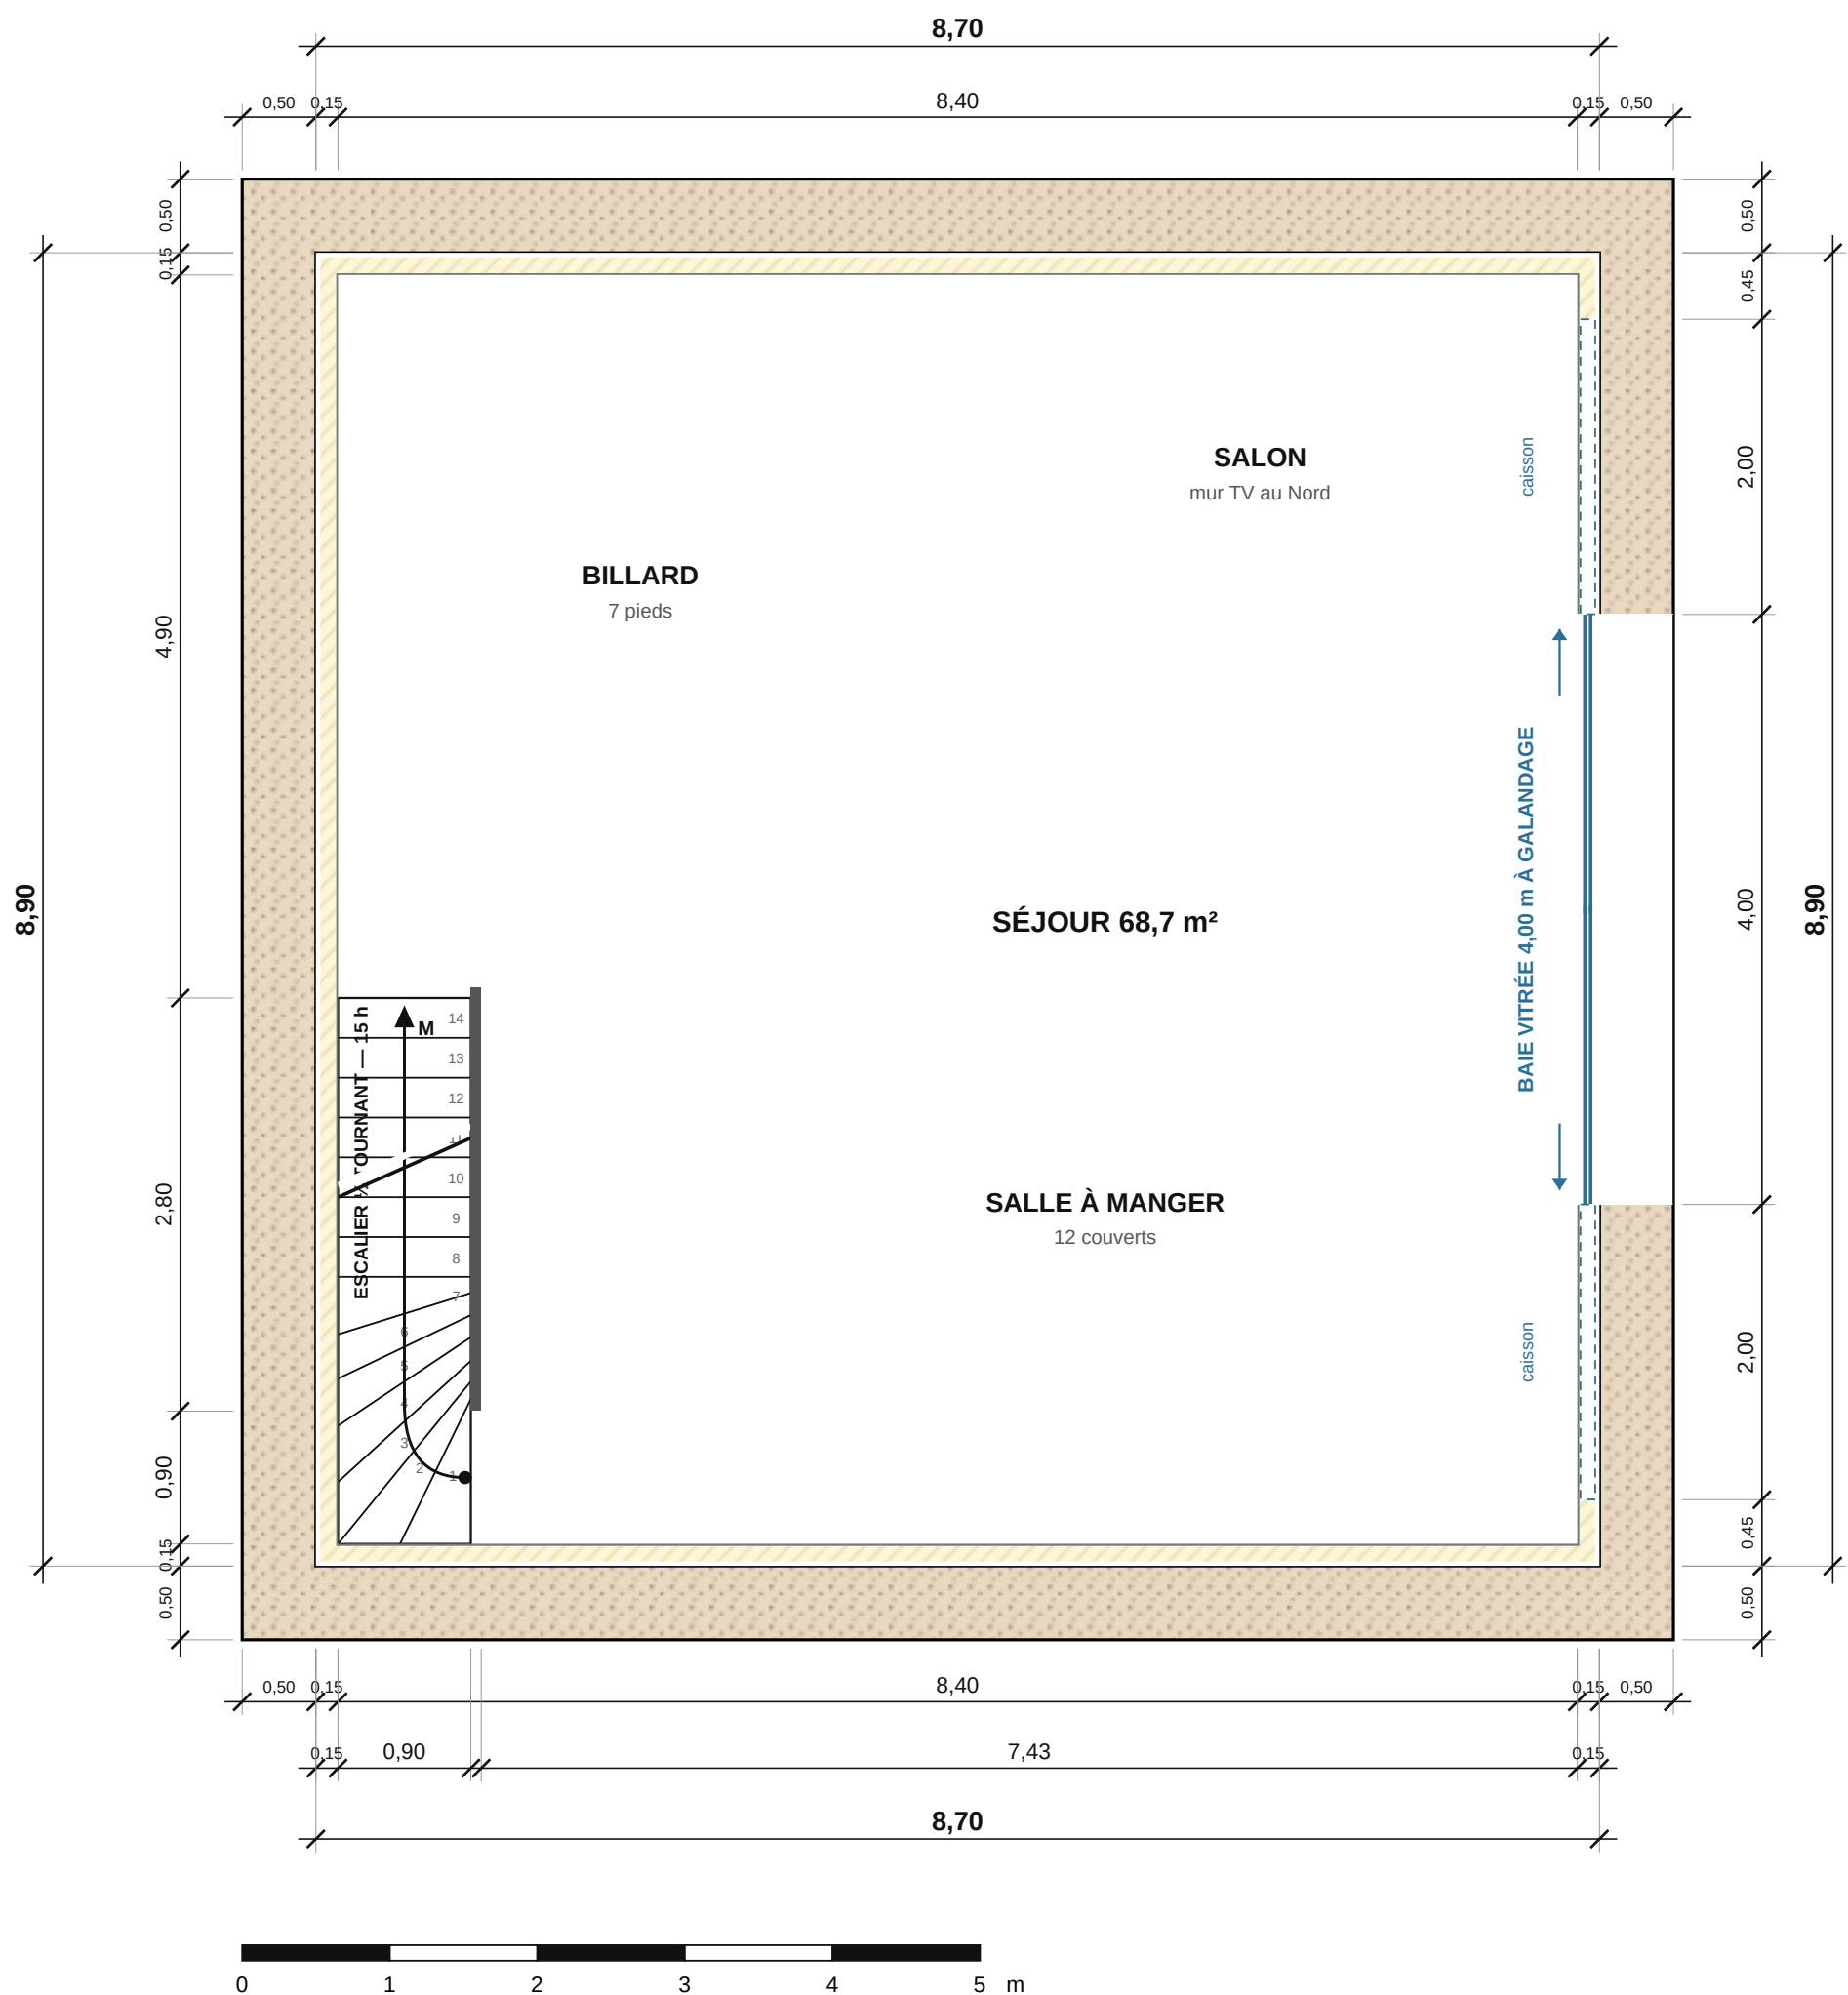


TABLEAU DES SURFACES

Séjour : salon + salle à manger	68,7 m²
Escalier (emprise)	3,3 m²
Total pièces (fini)	72,0 m²
Plateau murs nus 8,70 × 8,90 = 77,4 m²	
Intérieur fini (doublage 15) 8,40 × 8,60 = 72,2 m²	

NOTES

Murs pisé ≈ 50 cm + doublage 15 cm (lame d'air + isolant perspirant), comme à l'étage.
Façade vitrée Est (jardin) = accès : baie 4,00 m à galandage, 2 vantaux de 2,00 m dans les murs.
Ouverture 4 m dans le pisé : linteau béton ou acier, étude BET obligatoire. Repli : 3,00 m.
Escalier identique à l'étage (¼ tournant bas).
Salon en L face au mur TV (Nord), vue jardin : canapé d'angle + 2 fauteuils + 2 poufs ≈ 11 pl.
Recul canapé / TV ≈ 2,90 m (écran 75" possible).
Billard 7 pieds (2,30 × 1,30) : dégagements 1,10 à 1,65 m — queue courte côté Nord.
Table 3,40 × 1,05 : 12 couverts (5 + 5 + 2).
Enfilade mur Sud ; pas de cuisine au RDC.

Mur pisé existant	Doublage 15 (lame d'air)
Cloison neuve 7 cm	Baie vitrée galandage
Porte (P = passage)	Caisson galandage

PROJET
La Marinka — Rez-de-chaussée (77 m²)
Salon TV + billard + salle à manger 12 pers.

PLAN RDC — PROJET COTÉ

ÉCHELLE 1/50 (A3)	DATE 04/10/2026	INDICE C — esquisse
-----------------------------	---------------------------	-------------------------------

PLAN RDC — AMÉNAGEMENT

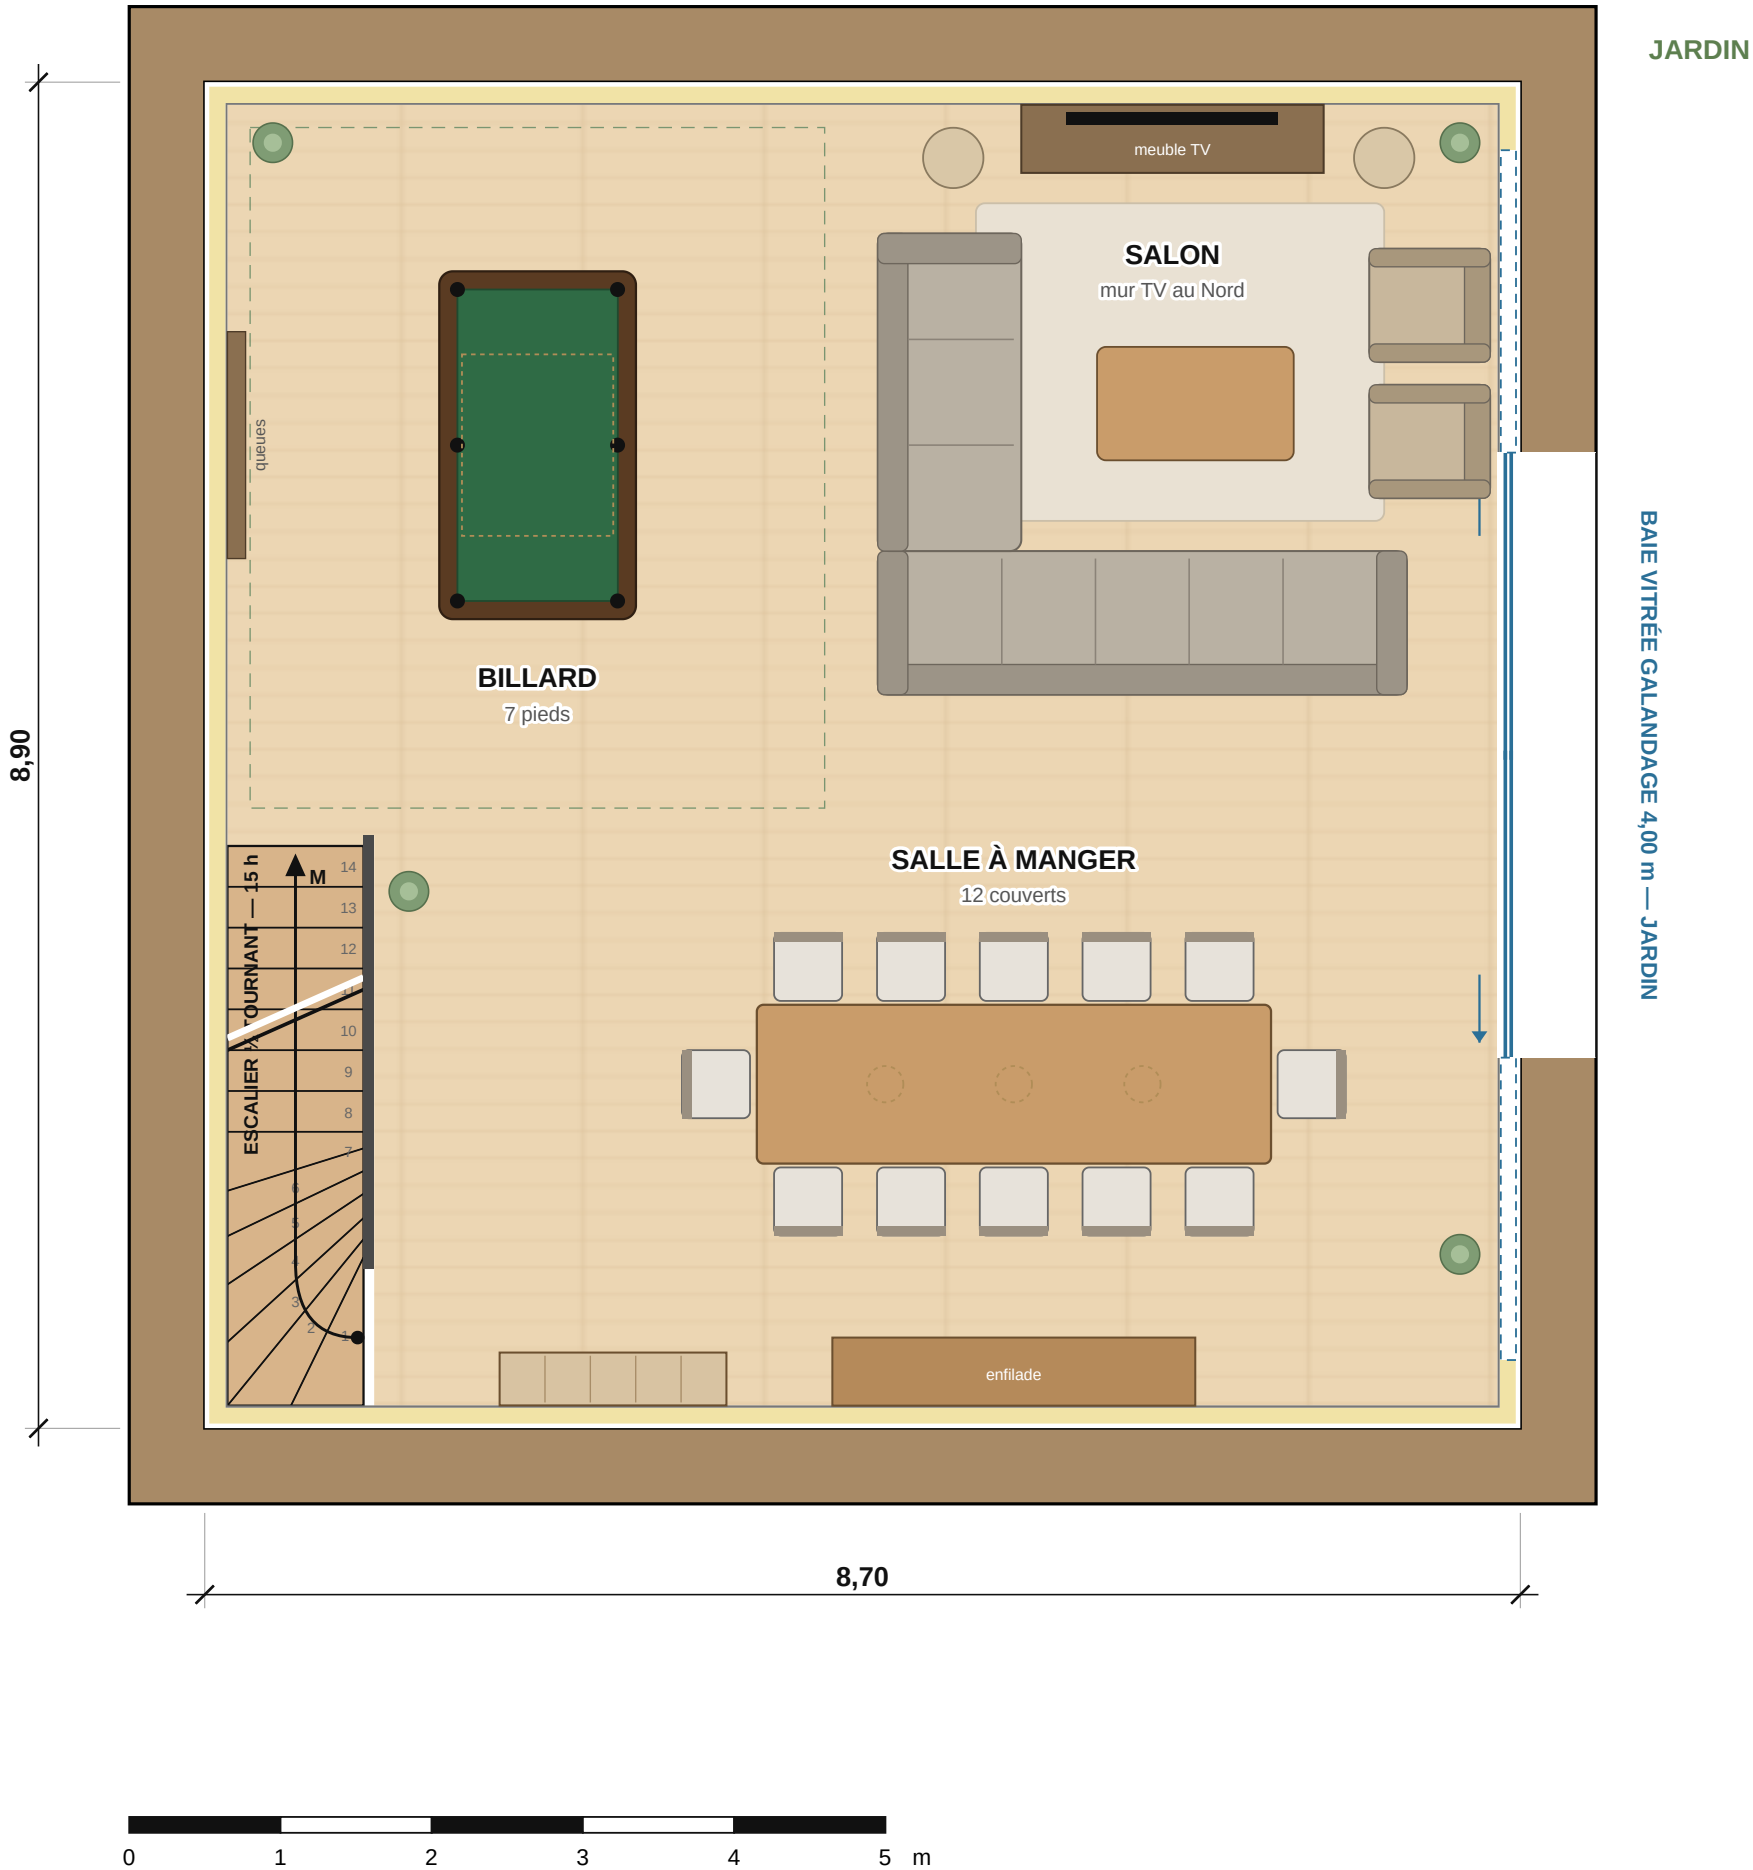


TABLEAU DES SURFACES

Séjour : salon + salle à manger	68,7 m²
Escalier (emprise)	3,3 m²
Total pièces (fini)	72,0 m²
Plateau murs nus 8,70 × 8,90 = 77,4 m²	
Intérieur fini (doublage 15) 8,40 × 8,60 = 72,2 m²	

NOTES

Murs pisé ≈ 50 cm + doublage 15 cm (lame d'air + isolant perspirant), comme à l'étage.
Façade vitrée Est (jardin) = accès : baie 4,00 m à galandage, 2 vantaux de 2,00 m dans les murs.
Ouverture 4 m dans le pisé : linteau béton ou acier, étude BET obligatoire. Repli : 3,00 m.
Escalier identique à l'étage (¼ tournant bas).
Salon en L face au mur TV (Nord), vue jardin : canapé d'angle + 2 fauteuils + 2 poufs ≈ 11 pl.
Recul canapé / TV ≈ 2,90 m (écran 75" possible).
Billard 7 pieds (2,30 × 1,30) : dégagements 1,10 à 1,65 m — queue courte côté Nord.
Table 3,40 × 1,05 : 12 couverts (5 + 5 + 2).
Enfilade mur Sud ; pas de cuisine au RDC.

Mur pisé existant	Doublage 15 (lame d'air)
Cloison neuve 7 cm	Baie vitrée galandage
Porte (P = passage)	Caisson galandage

PROJET
La Marinka — Rez-de-chaussée (77 m²)
Salon TV + billard + salle à manger 12 pers.

PLAN RDC — AMÉNAGEMENT

ÉCHELLE 1/50 (A3)	DATE 04/10/2026	INDICE C — esquisse
----------------------	--------------------	------------------------