

PLAN R+1 — PROJET COTÉ

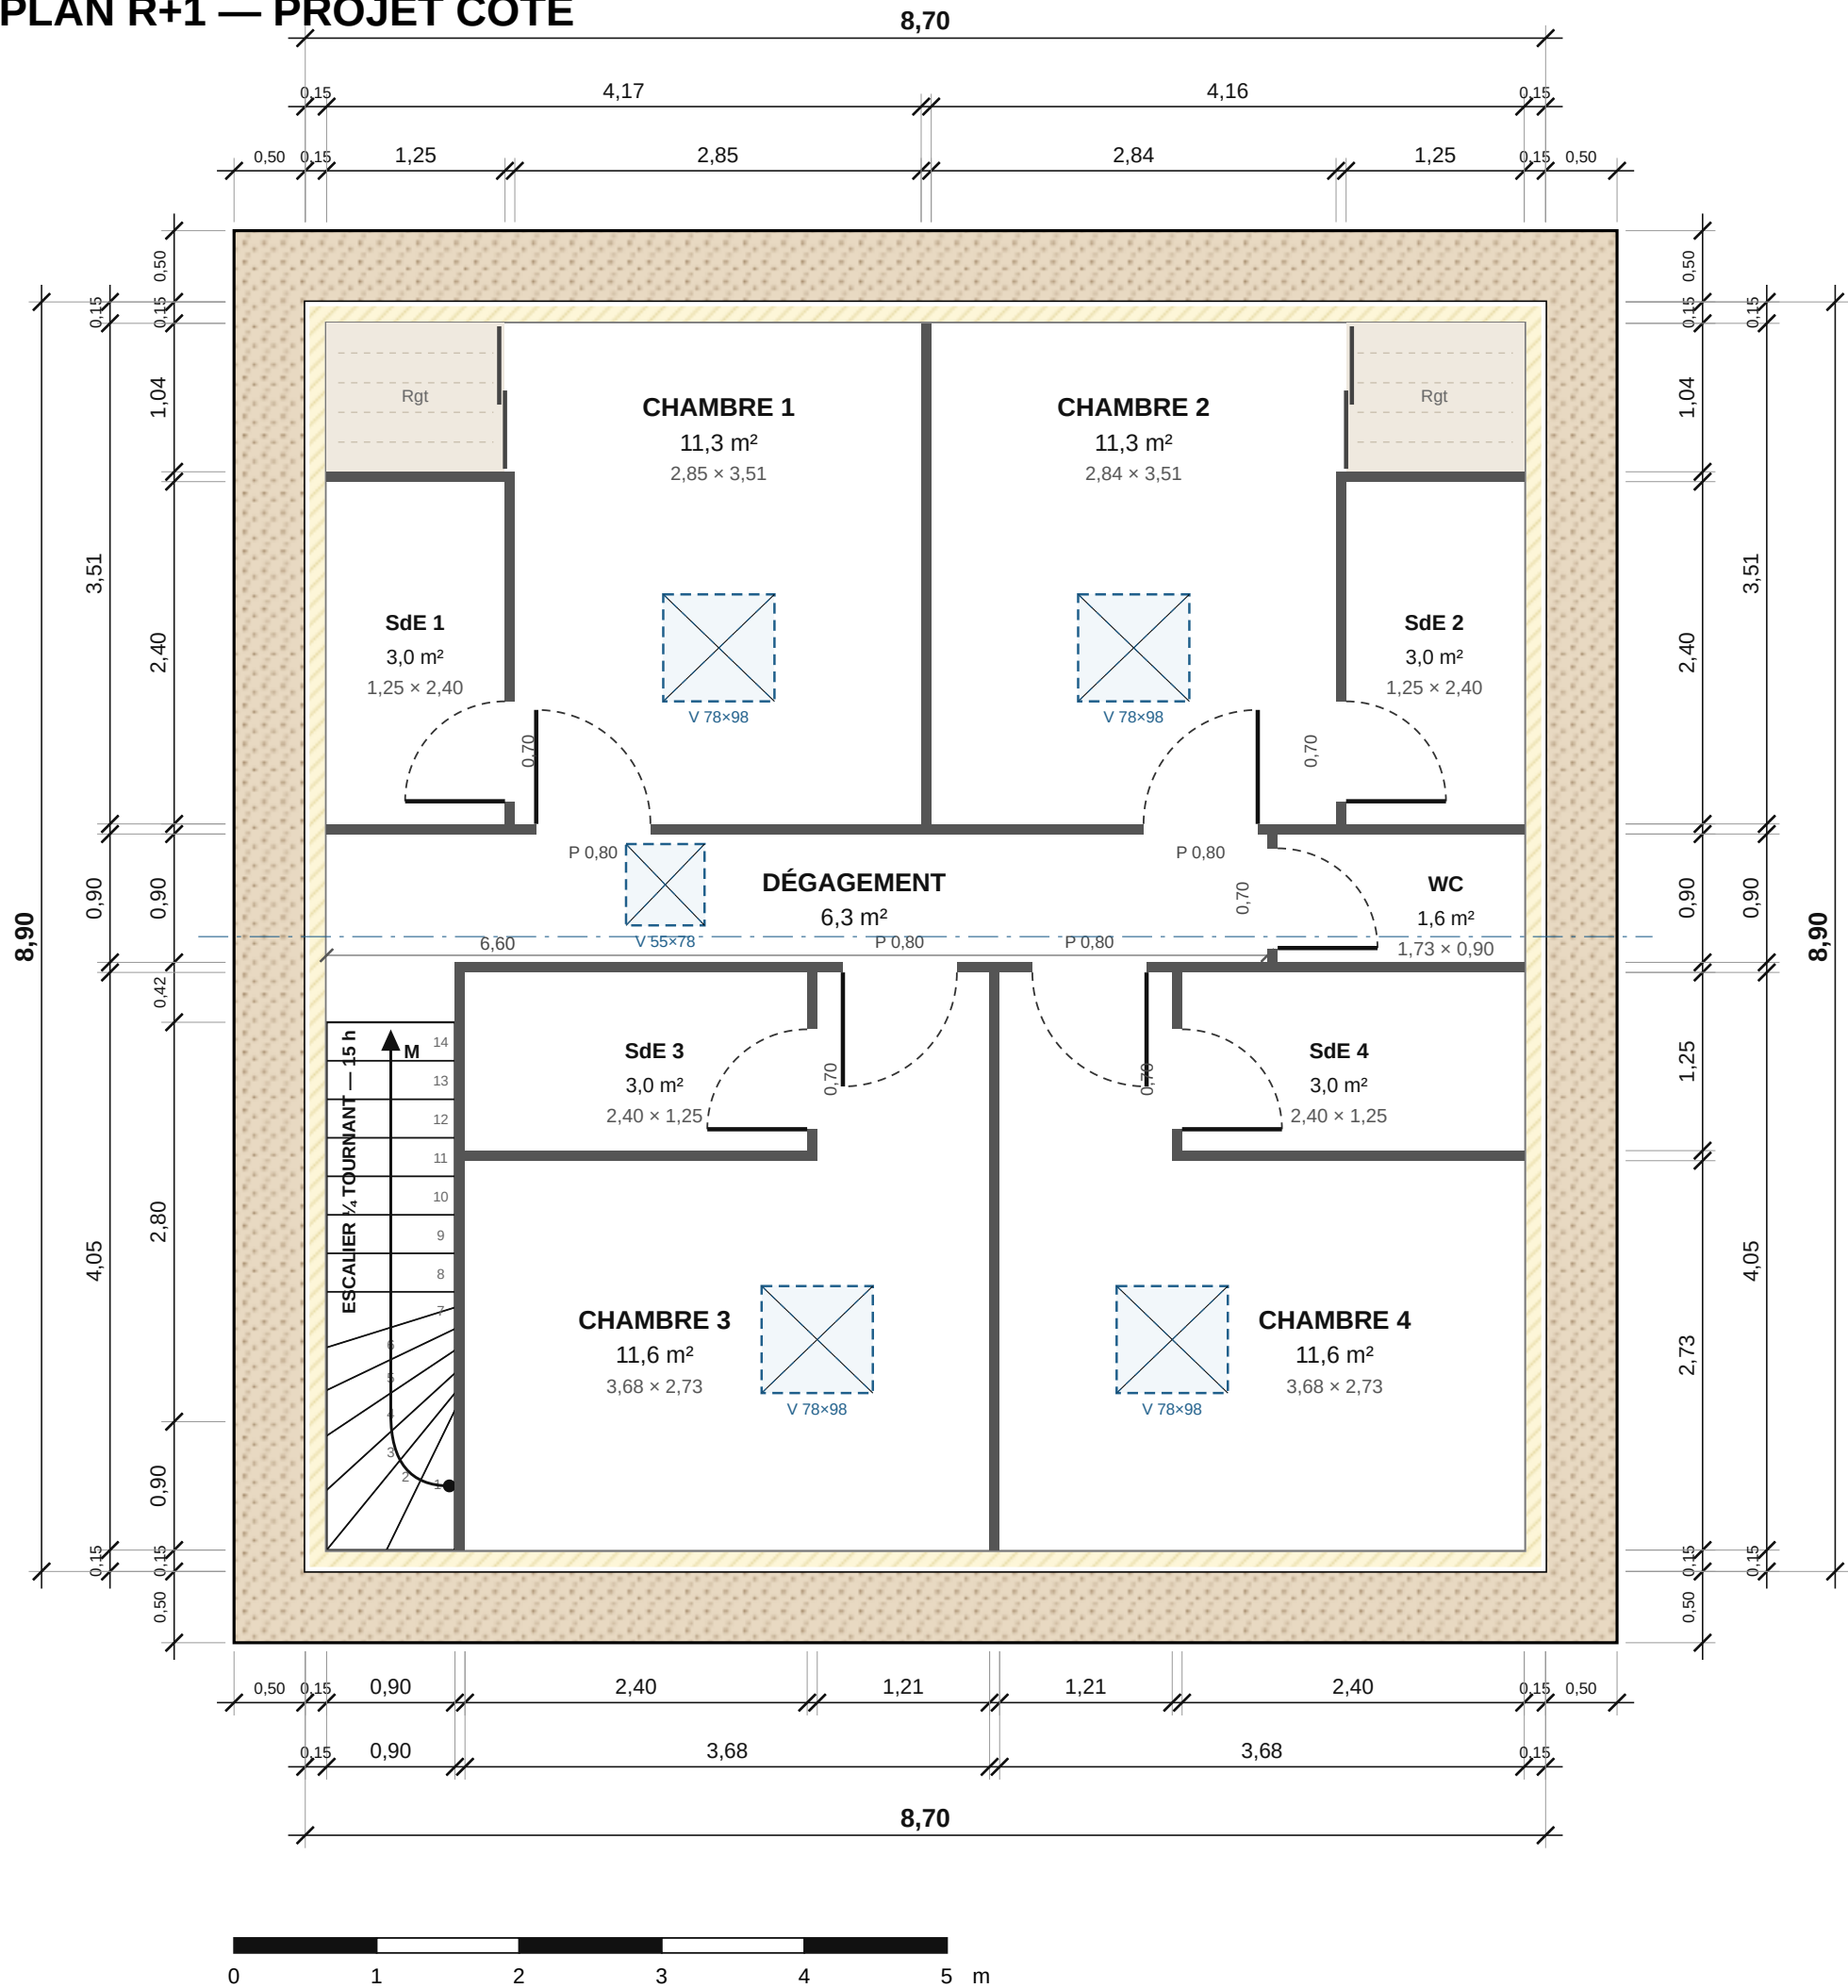


TABLEAU DES SURFACES

Chambre 1 (dont rangement 1,3)	11,3 m²
Chambre 2 (dont rangement 1,3)	11,3 m²
Chambre 3	11,6 m²
Chambre 4	11,6 m²
Salles d'eau 1 à 4 (4 × 3,0)	12,0 m²
WC indépendant	1,6 m²
Dégagement + palier	6,3 m²
Trémie escalier	3,3 m²
Total pièces (fini)	69,0 m²

Plateau murs nus 8,70 × 8,90 = 77,4 m²
Intérieur fini (double 15) 8,40 × 8,60 = 72,2 m²

NOTES

Murs en pisé ≈ 50 cm (épaisseur à relever).
Double 15 cm : lame d'air 3 cm + isolant perspirant (fibre de bois) 10 cm + frein-vapeur hygrovariable + placo 13 mm. Pas de pare-vapeur étanche : le pisé doit respirer.
Cloisons 7 cm (placo 72/48 + laine).
Escalier 1/4 tournant bas le long du mur Ouest : 15 h ≈ 19 cm, giron 27 cm, emmarchement 0,90.
Trémie 0,90 × 3,70 : avis structure / BET.
Velux : chambres + dégagement uniquement.
SdE et WC sans Velux : VMC hygro obligatoire.
SdE en longueur 1,25 × 2,40 : douche 120×80 au fond, vasque 75, sèche-serviettes.
Rangements bas sous rampant (ch. 1 et 2).
Faîtage E-O supposé ; zones < 1,80 m hors Carrez, à vérifier.

Mur pisé existant	Double 15 (lame d'air)
Cloison neuve 7 cm	Velux (projection)
Porte (P = passage)	Faîtage supposé

PROJET
Réaménagement de l'étage — 77 m²
4 chambres + 4 salles d'eau + WC indépendant

PLAN R+1 — PROJET COTÉ

ÉCHELLE 1/50 (A3)	DATE 04/10/2026	INDICE D — esquisse
----------------------	--------------------	------------------------

PLAN R+1 — AMÉNAGEMENT

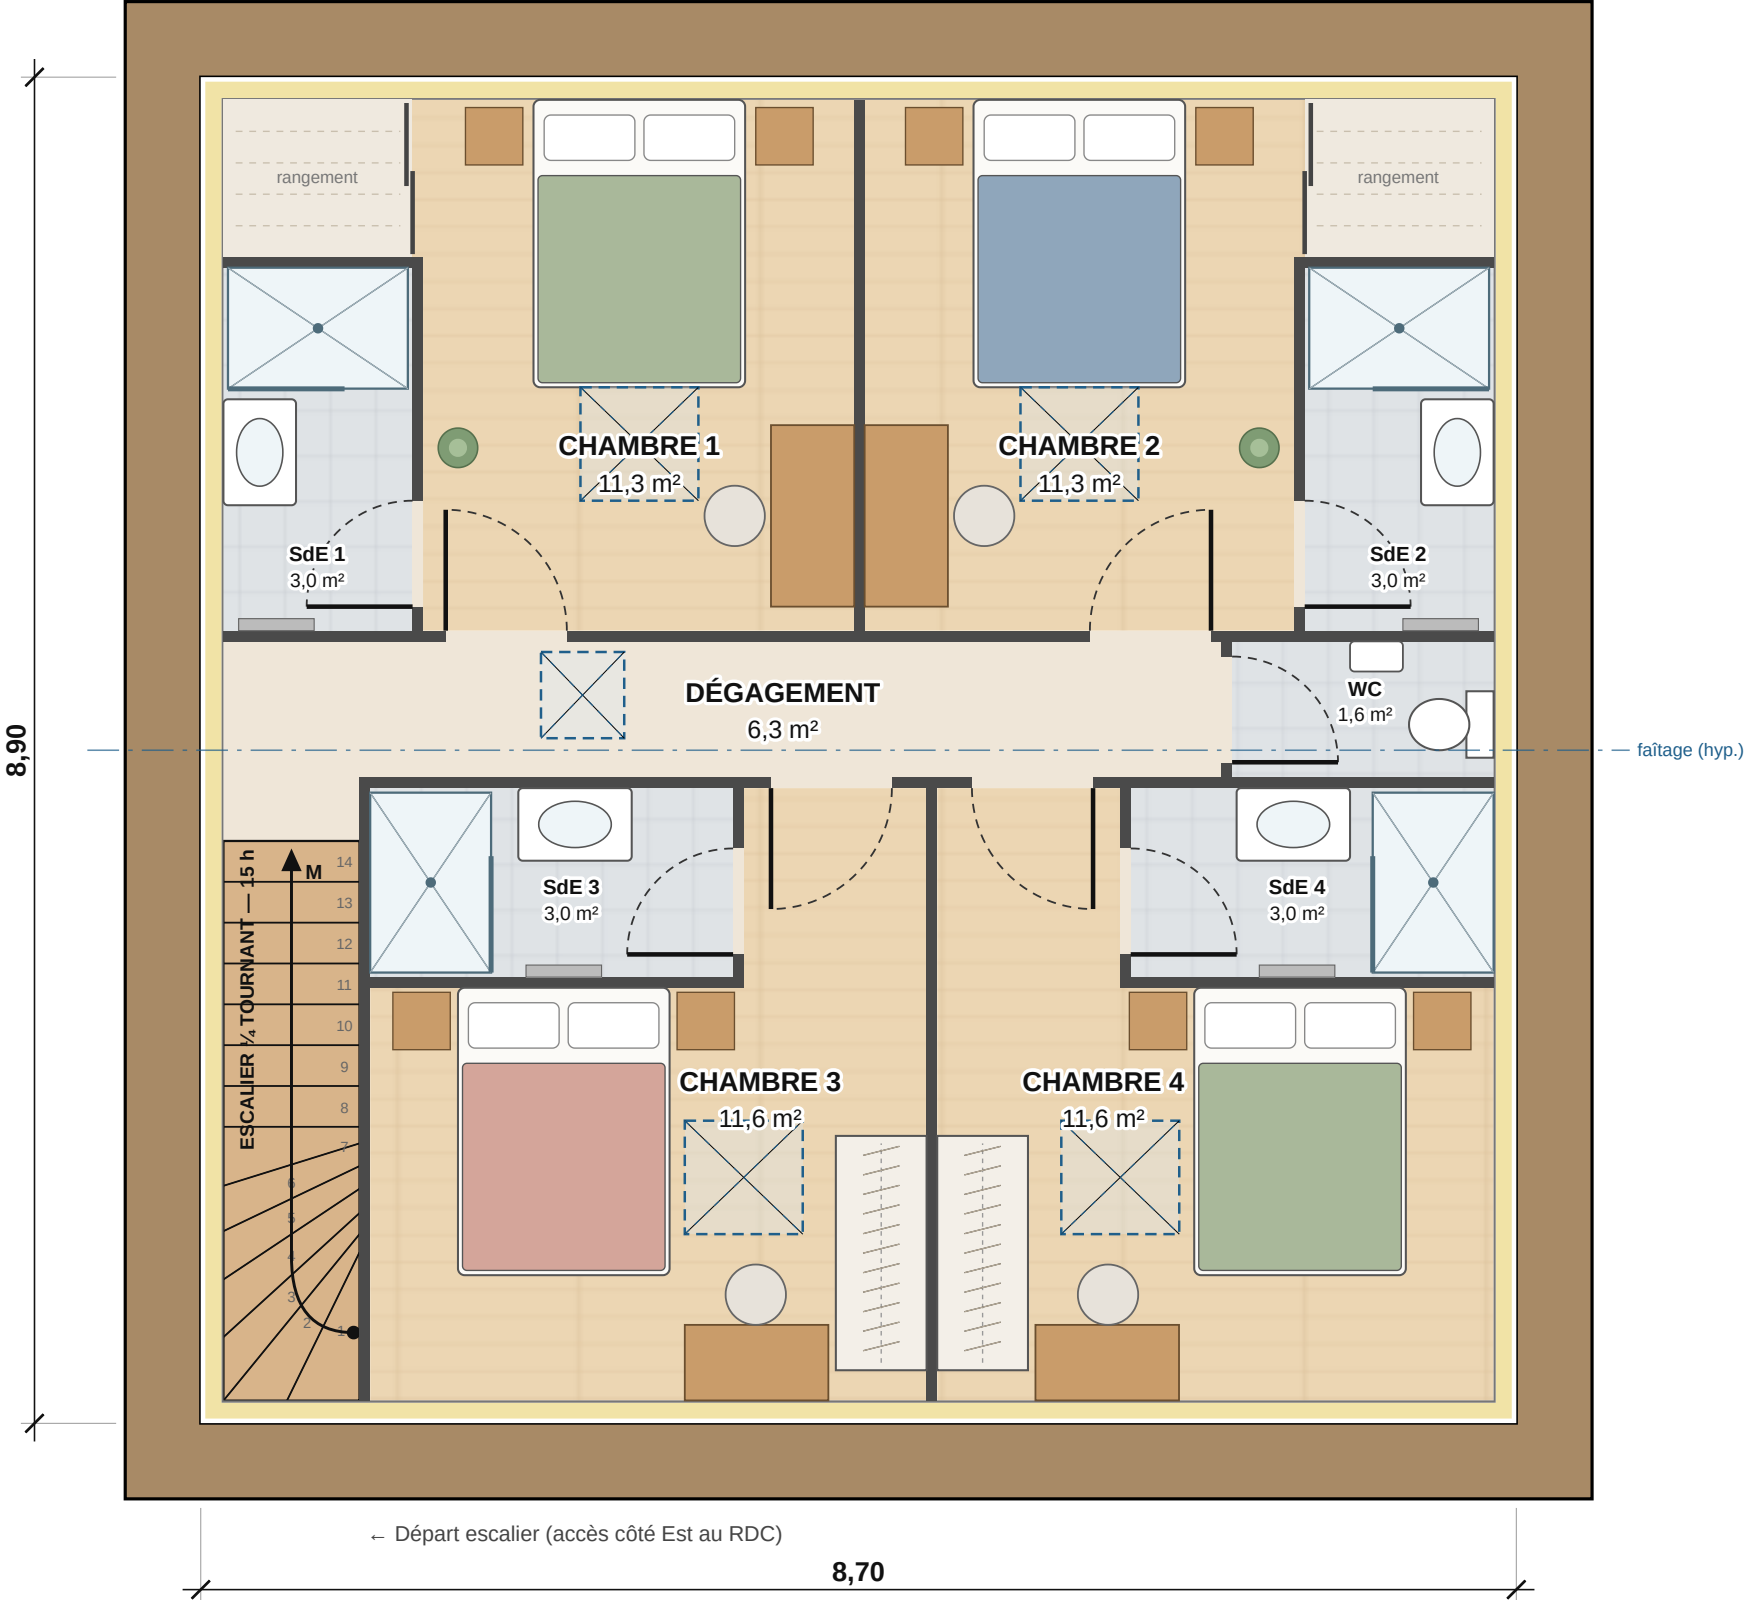


TABLEAU DES SURFACES

Chambre 1 (dont rangement 1,3)	11,3 m ²
Chambre 2 (dont rangement 1,3)	11,3 m ²
Chambre 3	11,6 m ²
Chambre 4	11,6 m ²
Salles d'eau 1 à 4 (4 × 3,0)	12,0 m ²
WC indépendant	1,6 m ²
Dégagement + palier	6,3 m ²
Trémie escalier	3,3 m ²
Total pièces (fini)	69,0 m²

Plateau murs nus 8,70 × 8,90 = 77,4 m²
Intérieur fini (doublage 15) 8,40 × 8,60 = 72,2 m²

NOTES

Murs en pisé ≈ 50 cm (épaisseur à relever).
Doublage 15 cm : lame d'air 3 cm + isolant perspirant (fibre de bois) 10 cm + frein-vapeur hydrovariable + placo 13 mm. Pas de pare-vapeur étanche : le pisé doit respirer.
Cloisons 7 cm (placo 72/48 + laine).
Escalier ¼ tournant bas le long du mur Ouest : 15 h ≈ 19 cm, giron 27 cm, emmarchement 0,90.
Trémie 0,90 × 3,70 : avis structure / BET.
Velux : chambres + dégagement uniquement.
SdE et WC sans Velux : VMC hygro obligatoire.
SdE en longueur 1,25 × 2,40 : douche 120×80 au fond, vasque 75, sèche-serviettes.
Rangements bas sous rampant (ch. 1 et 2).
Faîtage E-O supposé ; zones < 1,80 m hors Carrez, à vérifier.

Mur pisé existant	Doublage 15 (lame d'air)
Cloison neuve 7 cm	Velux (projection)
Porte (P = passage)	Faîtage supposé

PROJET
Réaménagement de l'étage — 77 m²
4 chambres + 4 salles d'eau + WC indépendant

PLAN R+1 — AMÉNAGEMENT

ÉCHELLE 1/50 (A3)	DATE 04/10/2026	INDICE D — esquisse
-----------------------------	---------------------------	-------------------------------