

PLAN R+1 — PROJET COTÉ

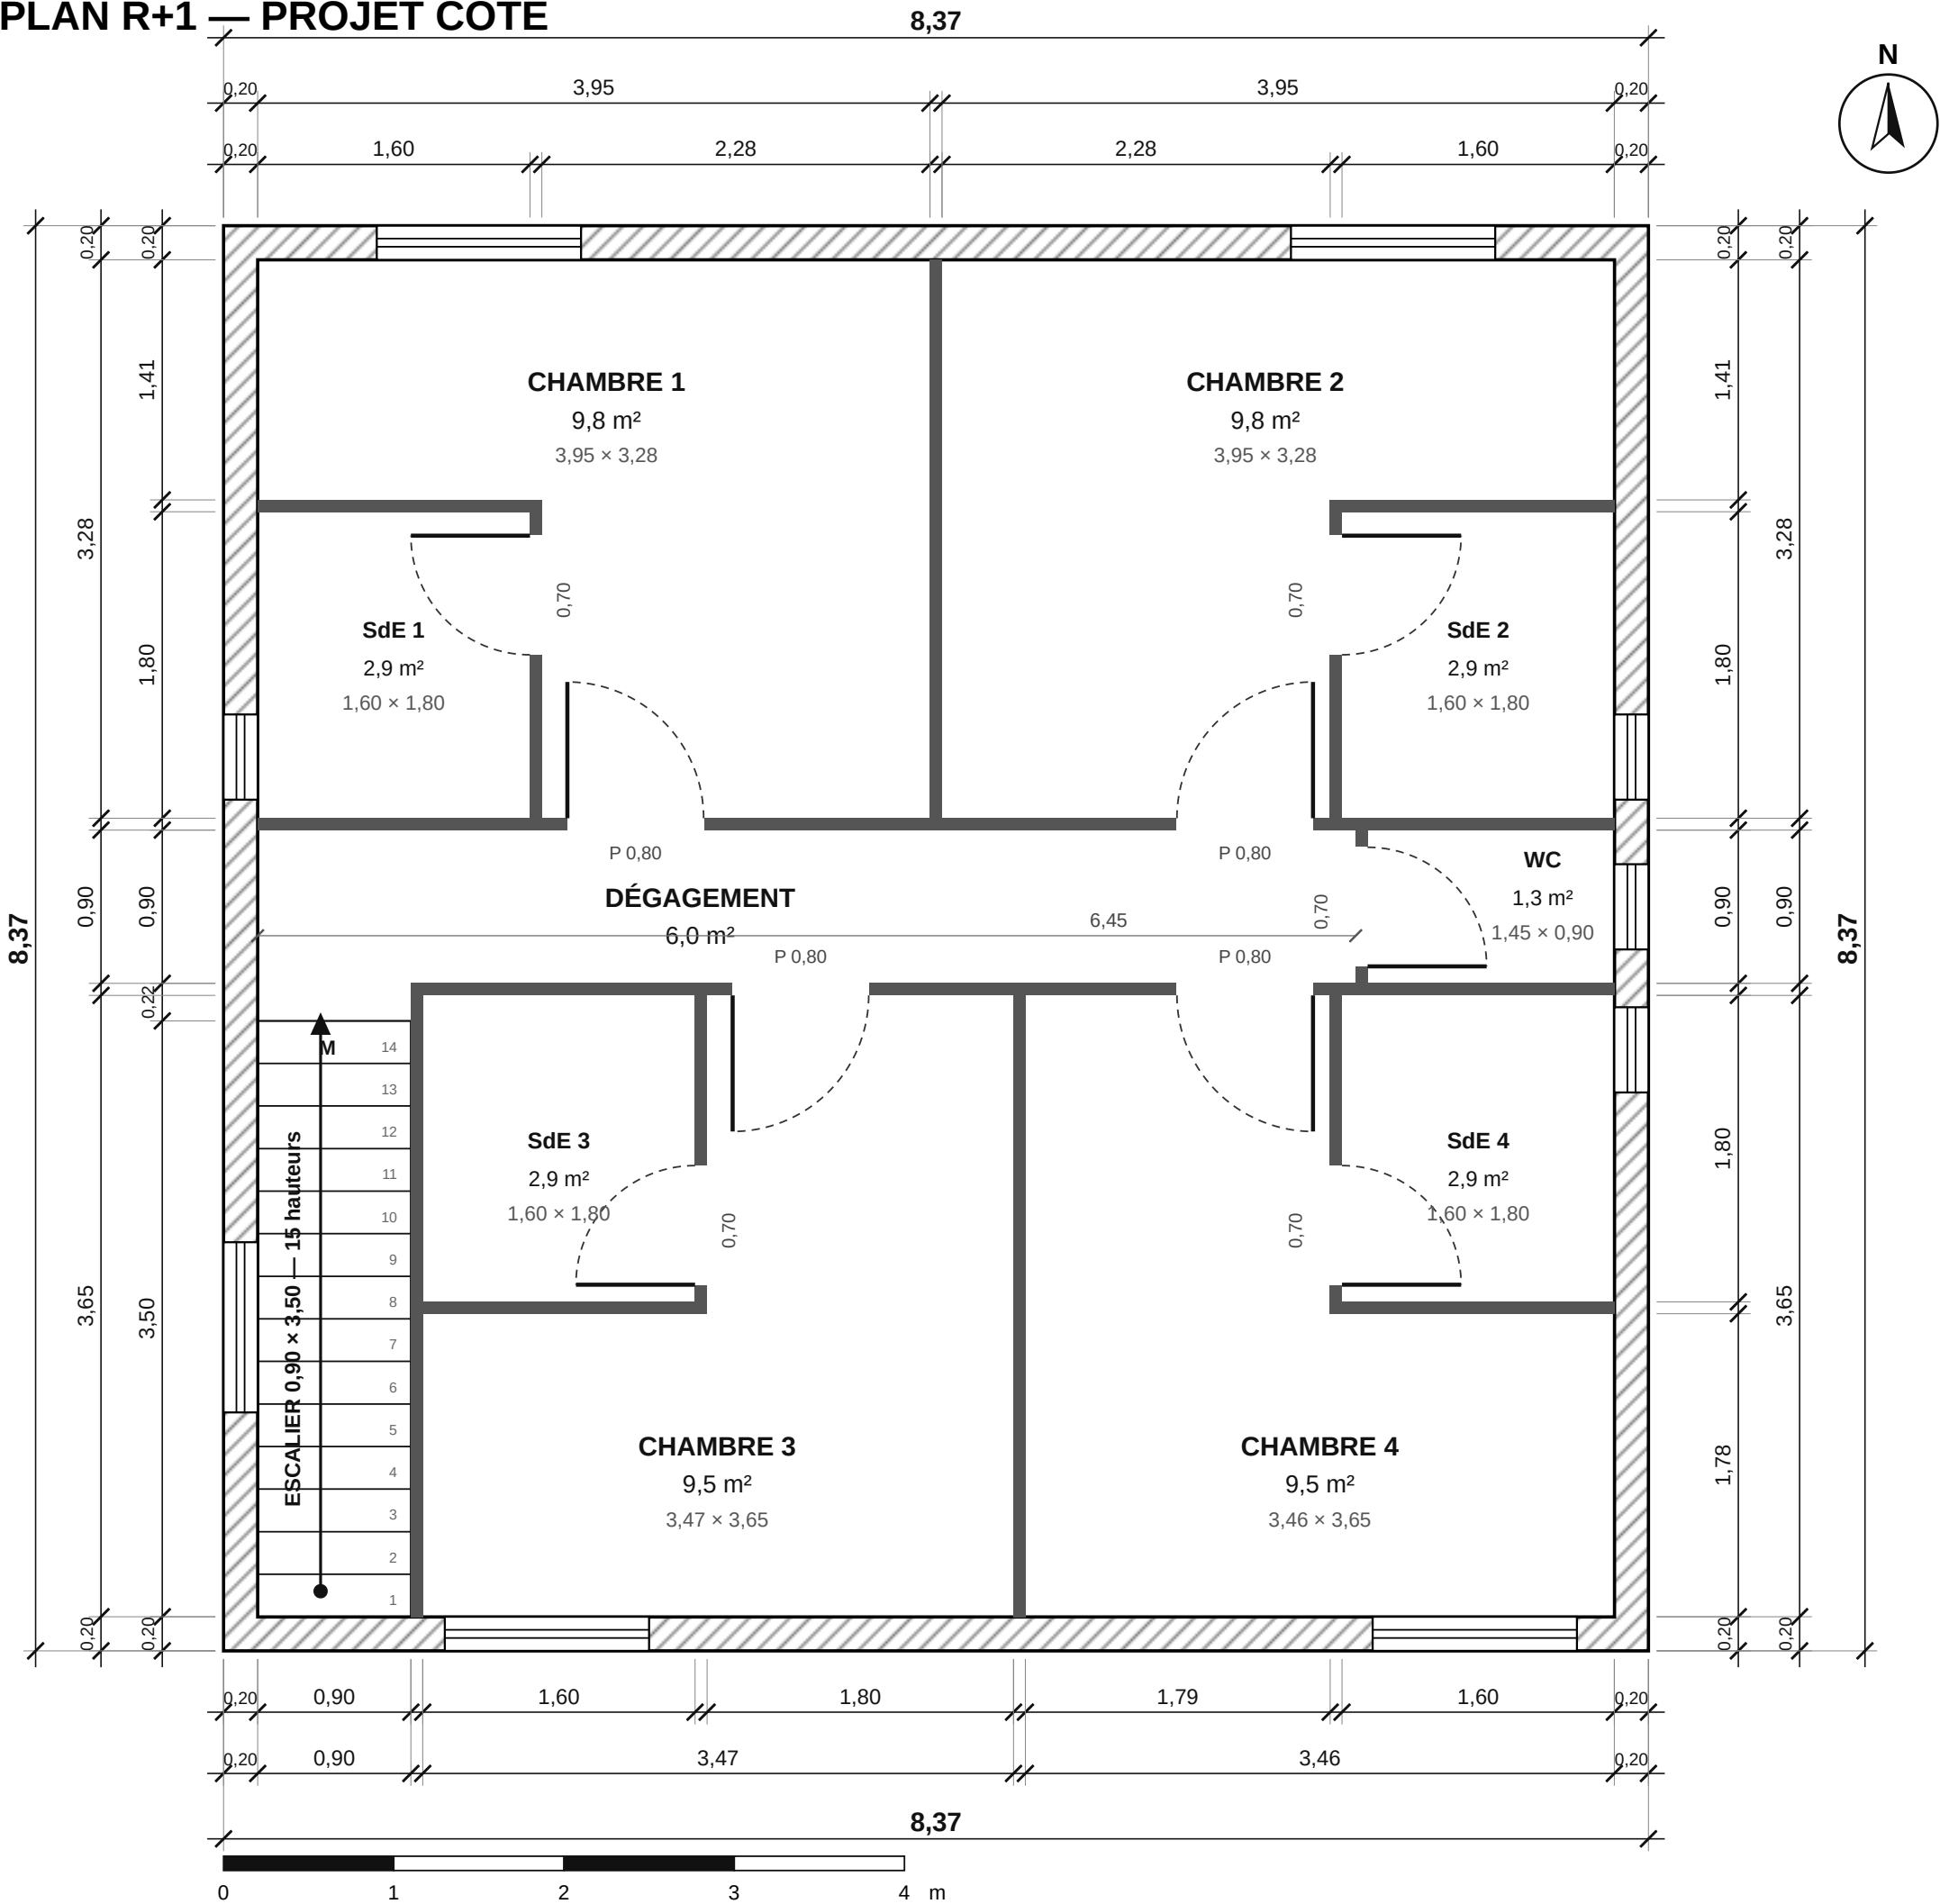


TABLEAU DES SURFACES

Chambre 1	9,8 m²
Chambre 2	9,8 m²
Chambre 3	9,5 m²
Chambre 4	9,5 m²
Salle d'eau 1	2,9 m²
Salle d'eau 2	2,9 m²
Salle d'eau 3	2,9 m²
Salle d'eau 4	2,9 m²
WC indépendant	1,3 m²
Dégagement + palier	6,0 m²
Trémie escalier	3,2 m²

Total pièces 60,7 m²

Intérieur murs ext. 7,97 x 7,97 = 63,5 m²
Emprise 8,37 x 8,37 = 70 m²

NOTES

Murs extérieurs 20 cm — cloisons 7 cm (type placo 72/48 + isolant phonique).
Cotes en mètres, intérieur brut de cloison.
Escalier droit le long du mur Ouest, départ en bas (Sud) : emmarchement 0,90, 14 girons de 25 cm, 15 hauteurs ≈ 19 cm (à recaler sur la hauteur d'étage réelle).
Nouvelle trémie 0,90 x 3,50 : reprise de plancher → avis structure / BET.
Salles d'eau : douche 90 x 120 extra-plate, vasque 80, sèche-serviettes, VMC hygro.
SdE 3 sans fenêtre : extraction VMC.
WC suspendu + lave-mains, fenêtre Est.
Gaine technique Est : SdE 2 + WC + SdE 4 regroupés (chute Ø100).
Fenêtres indicatives : à caler sur les baies existantes.

Mur ext. conservé	Cloison neuve 7 cm
Fenêtre	Porte (P = passage)

PROJET
Réaménagement de l'étage — 70 m²
4 chambres + 4 salles d'eau + WC indépendant

PLAN R+1 — PROJET COTÉ

ÉCHELLE 1/40 (A3)	DATE 04/10/2026	INDICE A — esquisse
----------------------	--------------------	------------------------

PLAN R+1 — AMÉNAGEMENT



TABLEAU DES SURFACES

Chambre 1	9,8 m ²
Chambre 2	9,8 m ²
Chambre 3	9,5 m ²
Chambre 4	9,5 m ²
Salle d'eau 1	2,9 m ²
Salle d'eau 2	2,9 m ²
Salle d'eau 3	2,9 m ²
Salle d'eau 4	2,9 m ²
WC indépendant	1,3 m ²
Dégagement + palier	6,0 m ²
Trémie escalier	3,2 m ²

Total pièces 60,7 m²

Intérieur murs ext. 7,97 x 7,97 = 63,5 m²
Emprise 8,37 x 8,37 = 70 m²

NOTES

Murs extérieurs 20 cm — cloisons 7 cm (type placo 72/48 + isolant phonique).
Cotes en mètres, intérieur brut de cloison.
Escalier droit le long du mur Ouest, départ en bas (Sud) : emmarchement 0,90, 14 girons de 25 cm, 15 hauteurs ≈ 19 cm (à recaler sur la hauteur d'étage réelle).
Nouvelle trémie 0,90 x 3,50 : reprise de plancher → avis structure / BET.
Salles d'eau : douche 90 x 120 extra-plate, vasque 80, sèche-serviettes, VMC hygro.
SdE 3 sans fenêtre : extraction VMC.
WC suspendu + lave-mains, fenêtre Est.
Gaine technique Est : SdE 2 + WC + SdE 4 regroupés (chute Ø100).
Fenêtres indicatives : à caler sur les baies existantes.

Mur ext. conservé	Cloison neuve 7 cm
Fenêtre	Porte (P = passage)

PROJET
Réaménagement de l'étage — 70 m²
4 chambres + 4 salles d'eau + WC indépendant

PLAN R+1 — AMÉNAGEMENT

ÉCHELLE 1/40 (A3)	DATE 04/10/2026	INDICE A — esquisse
----------------------	--------------------	------------------------