

PLAN RDC — PROJET COTÉ

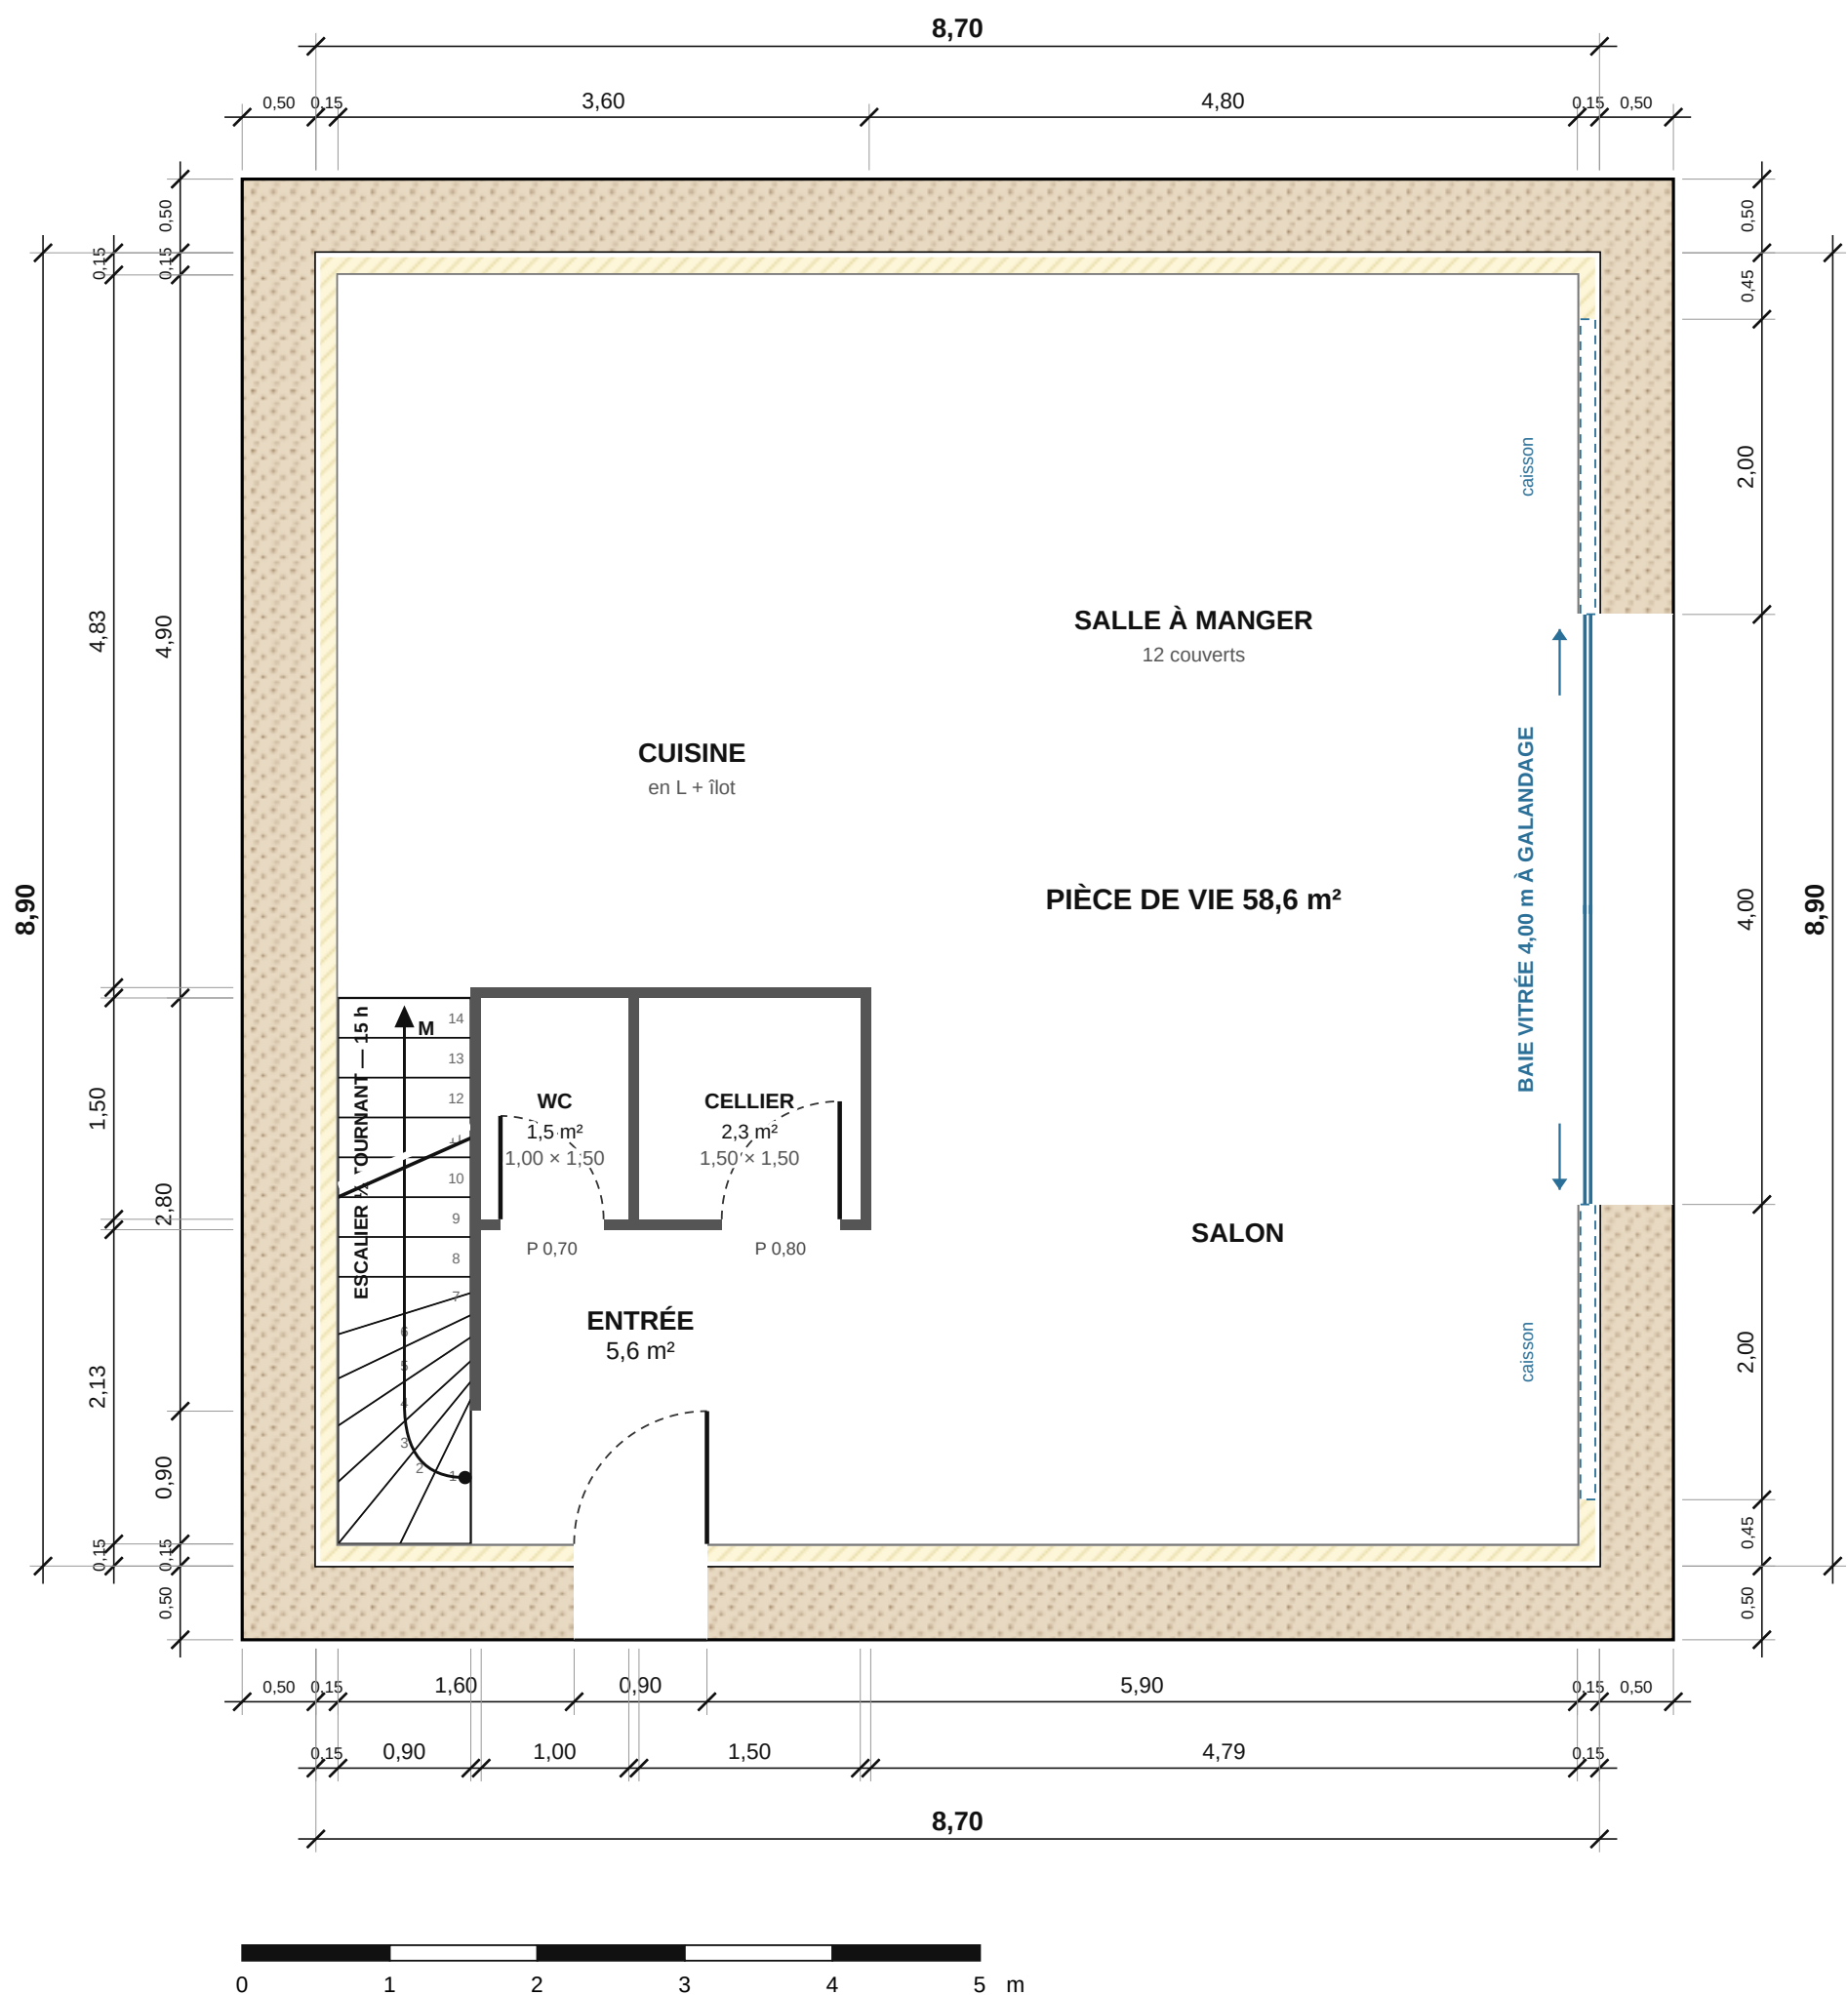


TABLEAU DES SURFACES

Pièce de vie (cuisine, séjour, salon)	58,6 m²
Entrée (dont placard)	5,6 m²
WC	1,5 m²
Cellier / buanderie	2,3 m²
Escalier (emprise)	3,3 m²
Total pièces (fini)	71,3 m²
Plateau murs nus 8,70 × 8,90 = 77,4 m²	
Intérieur fini (doublage 15) 8,40 × 8,60 = 72,2 m²	

NOTES

Murs pisé ≈ 50 cm + doublage 15 cm (lame d'air + isolant perspirant), comme à l'étage.
Baie vitrée 4,00 m à galandage, mur Est (jardin) : 2 vantaux de 2,00 m dans les murs.
Ouverture 4 m dans le pisé : linteau béton ou acier, étude BET obligatoire. Repli : 3,00 m.
Caissons : doublage épaissi local (≈ 20 cm).
Escalier identique à l'étage (¼ tournant bas).
Salon 10-12 pl. : canapés 3,60 + 3,20 + poufs.
Table 3,40 × 1,05 : 12 couverts (5 + 5 + 2).
Cuisine en L + îlot ; évier sous la chute Ouest.
WC + cellier sous la SdE 3 (chute commune).
Entrée au Sud (position à confirmer) ; autres ouvertures à reporter selon l'existant.

Mur pisé existant	Doublage 15 (lame d'air)
Cloison neuve 7 cm	Baie vitrée galandage
Porte (P = passage)	Caisson galandage

PROJET
La Marinka — Rez-de-chaussée (77 m²)
Séjour 12 pers. + cuisine + baie jardin

PLAN RDC — PROJET COTÉ

ÉCHELLE 1/50 (A3)	DATE 04/10/2026	INDICE A — esquisse
-----------------------------	---------------------------	-------------------------------

PLAN RDC — AMÉNAGEMENT

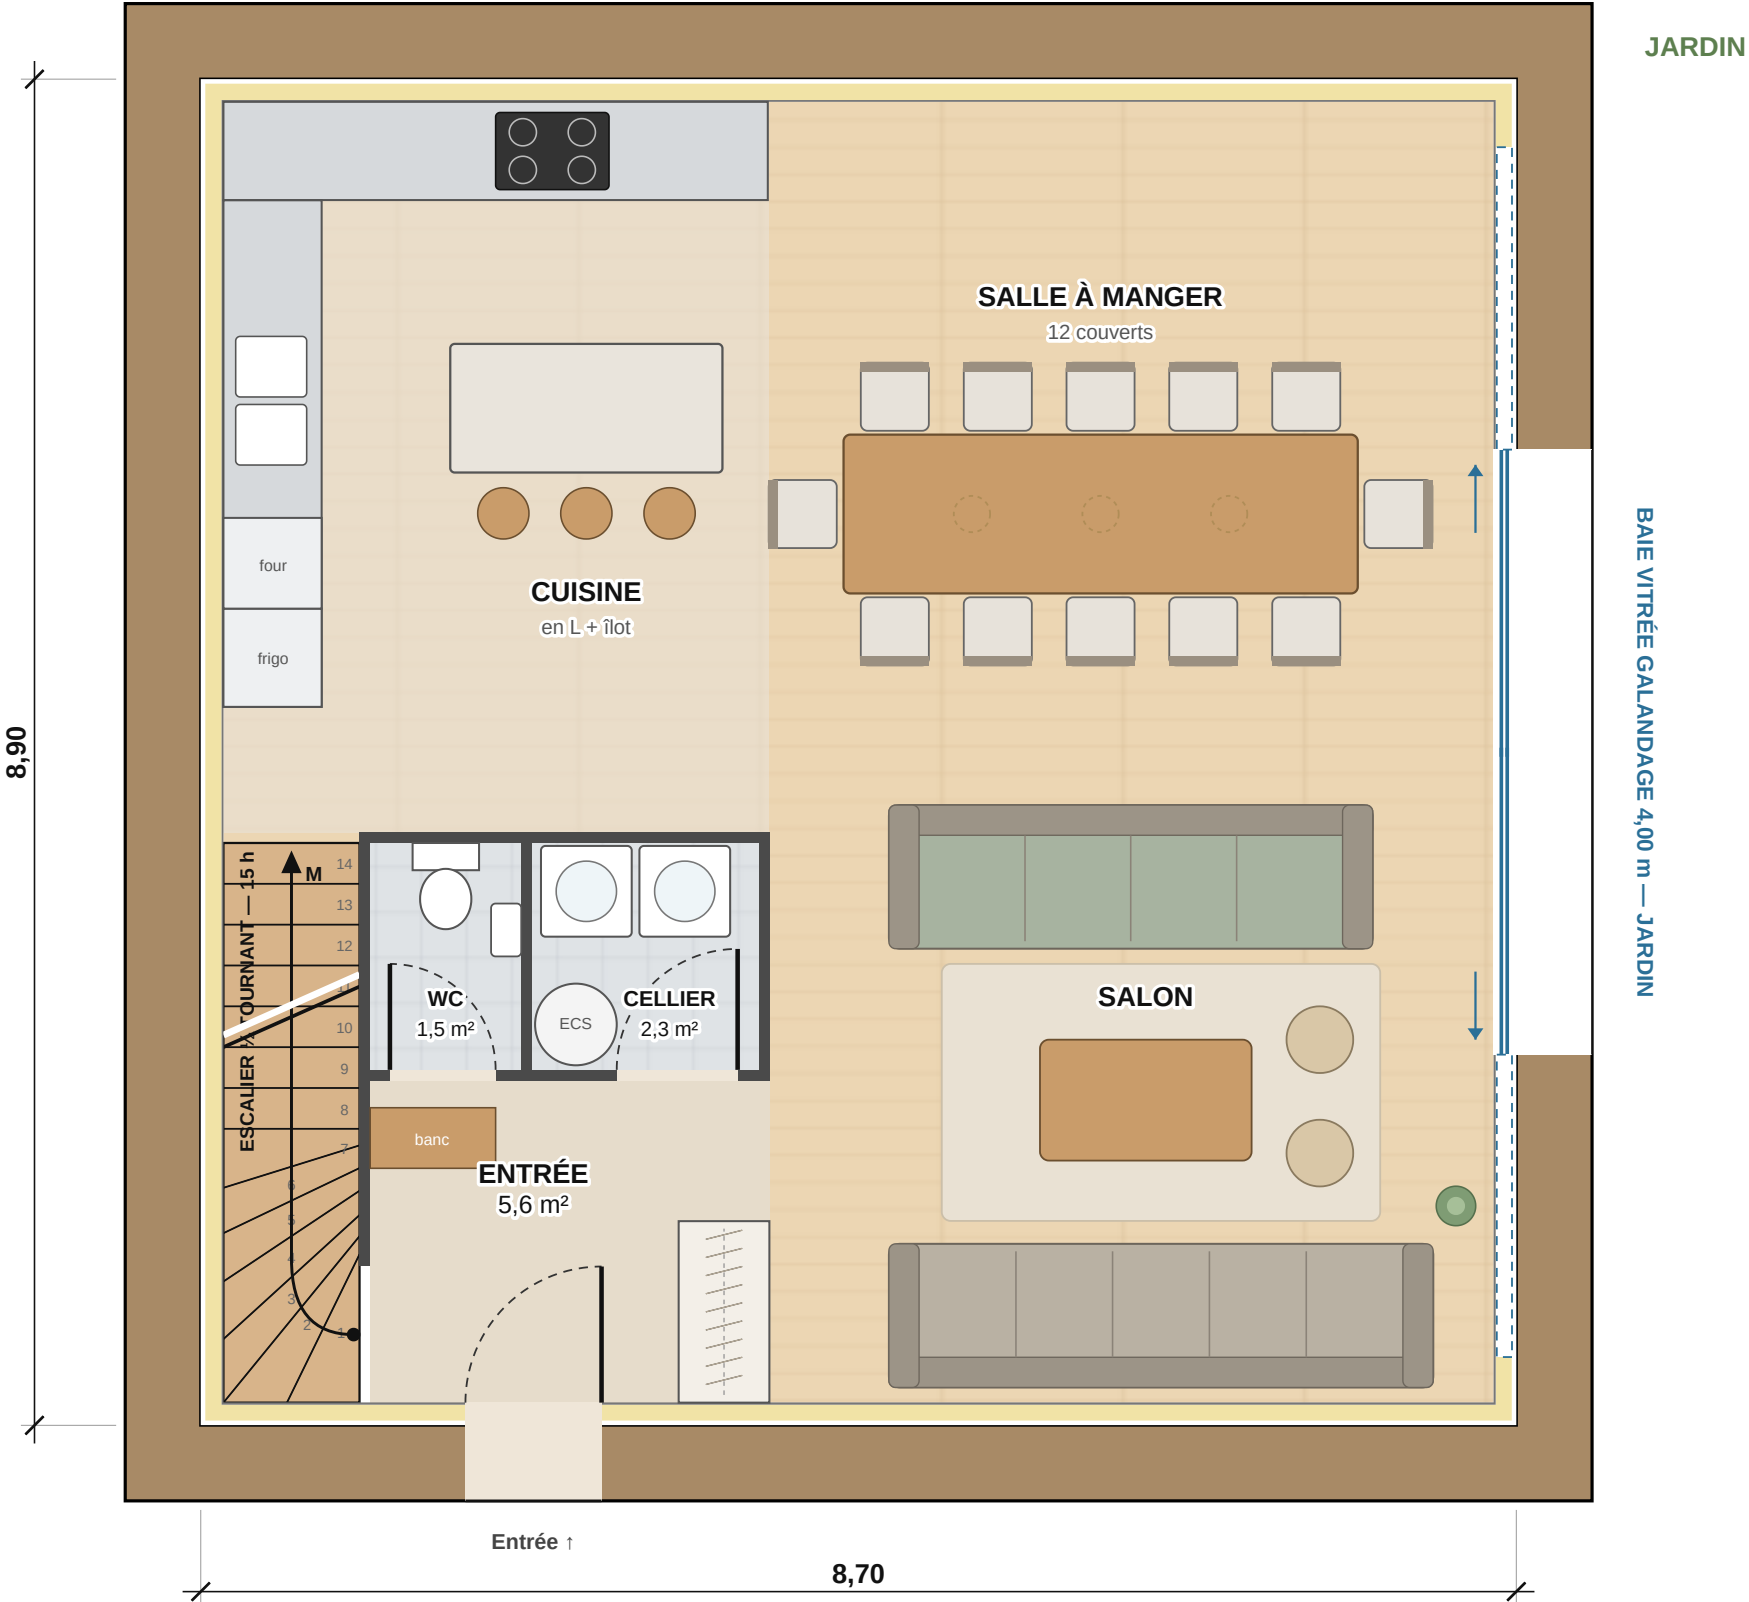


TABLEAU DES SURFACES

Pièce de vie (cuisine, séjour, salon)	58,6 m²
Entrée (dont placard)	5,6 m²
WC	1,5 m²
Cellier / buanderie	2,3 m²
Escalier (emprise)	3,3 m²
Total pièces (fini)	71,3 m²
Plateau murs nus 8,70 × 8,90 = 77,4 m²	
Intérieur fini (doublage 15) 8,40 × 8,60 = 72,2 m²	

NOTES

Murs pisé ≈ 50 cm + doublage 15 cm (lame d'air + isolant perspirant), comme à l'étage.
Baie vitrée 4,00 m à galandage, mur Est (jardin) : 2 vantaux de 2,00 m dans les murs.
Ouverture 4 m dans le pisé : linteau béton ou acier, étude BET obligatoire. Repli : 3,00 m.
Caissons : doublage épaissi local (≈ 20 cm).
Escalier identique à l'étage (¼ tournant bas).
Salon 10-12 pl. : canapés 3,60 + 3,20 + poufs.
Table 3,40 × 1,05 : 12 couverts (5 + 5 + 2).
Cuisine en L + îlot ; évier sous la chute Ouest.
WC + cellier sous la SdE 3 (chute commune).
Entrée au Sud (position à confirmer) ; autres ouvertures à reporter selon l'existant.

Mur pisé existant	Doublage 15 (lame d'air)
Cloison neuve 7 cm	Baie vitrée galandage
Porte (P = passage)	Caisson galandage

PROJET
La Marinka — Rez-de-chaussée (77 m²)
Séjour 12 pers. + cuisine + baie jardin

PLAN RDC — AMÉNAGEMENT

ÉCHELLE 1/50 (A3)	DATE 04/10/2026	INDICE A — esquisse
-----------------------------	---------------------------	-------------------------------