

PLAN RDC — PROJET COTÉ

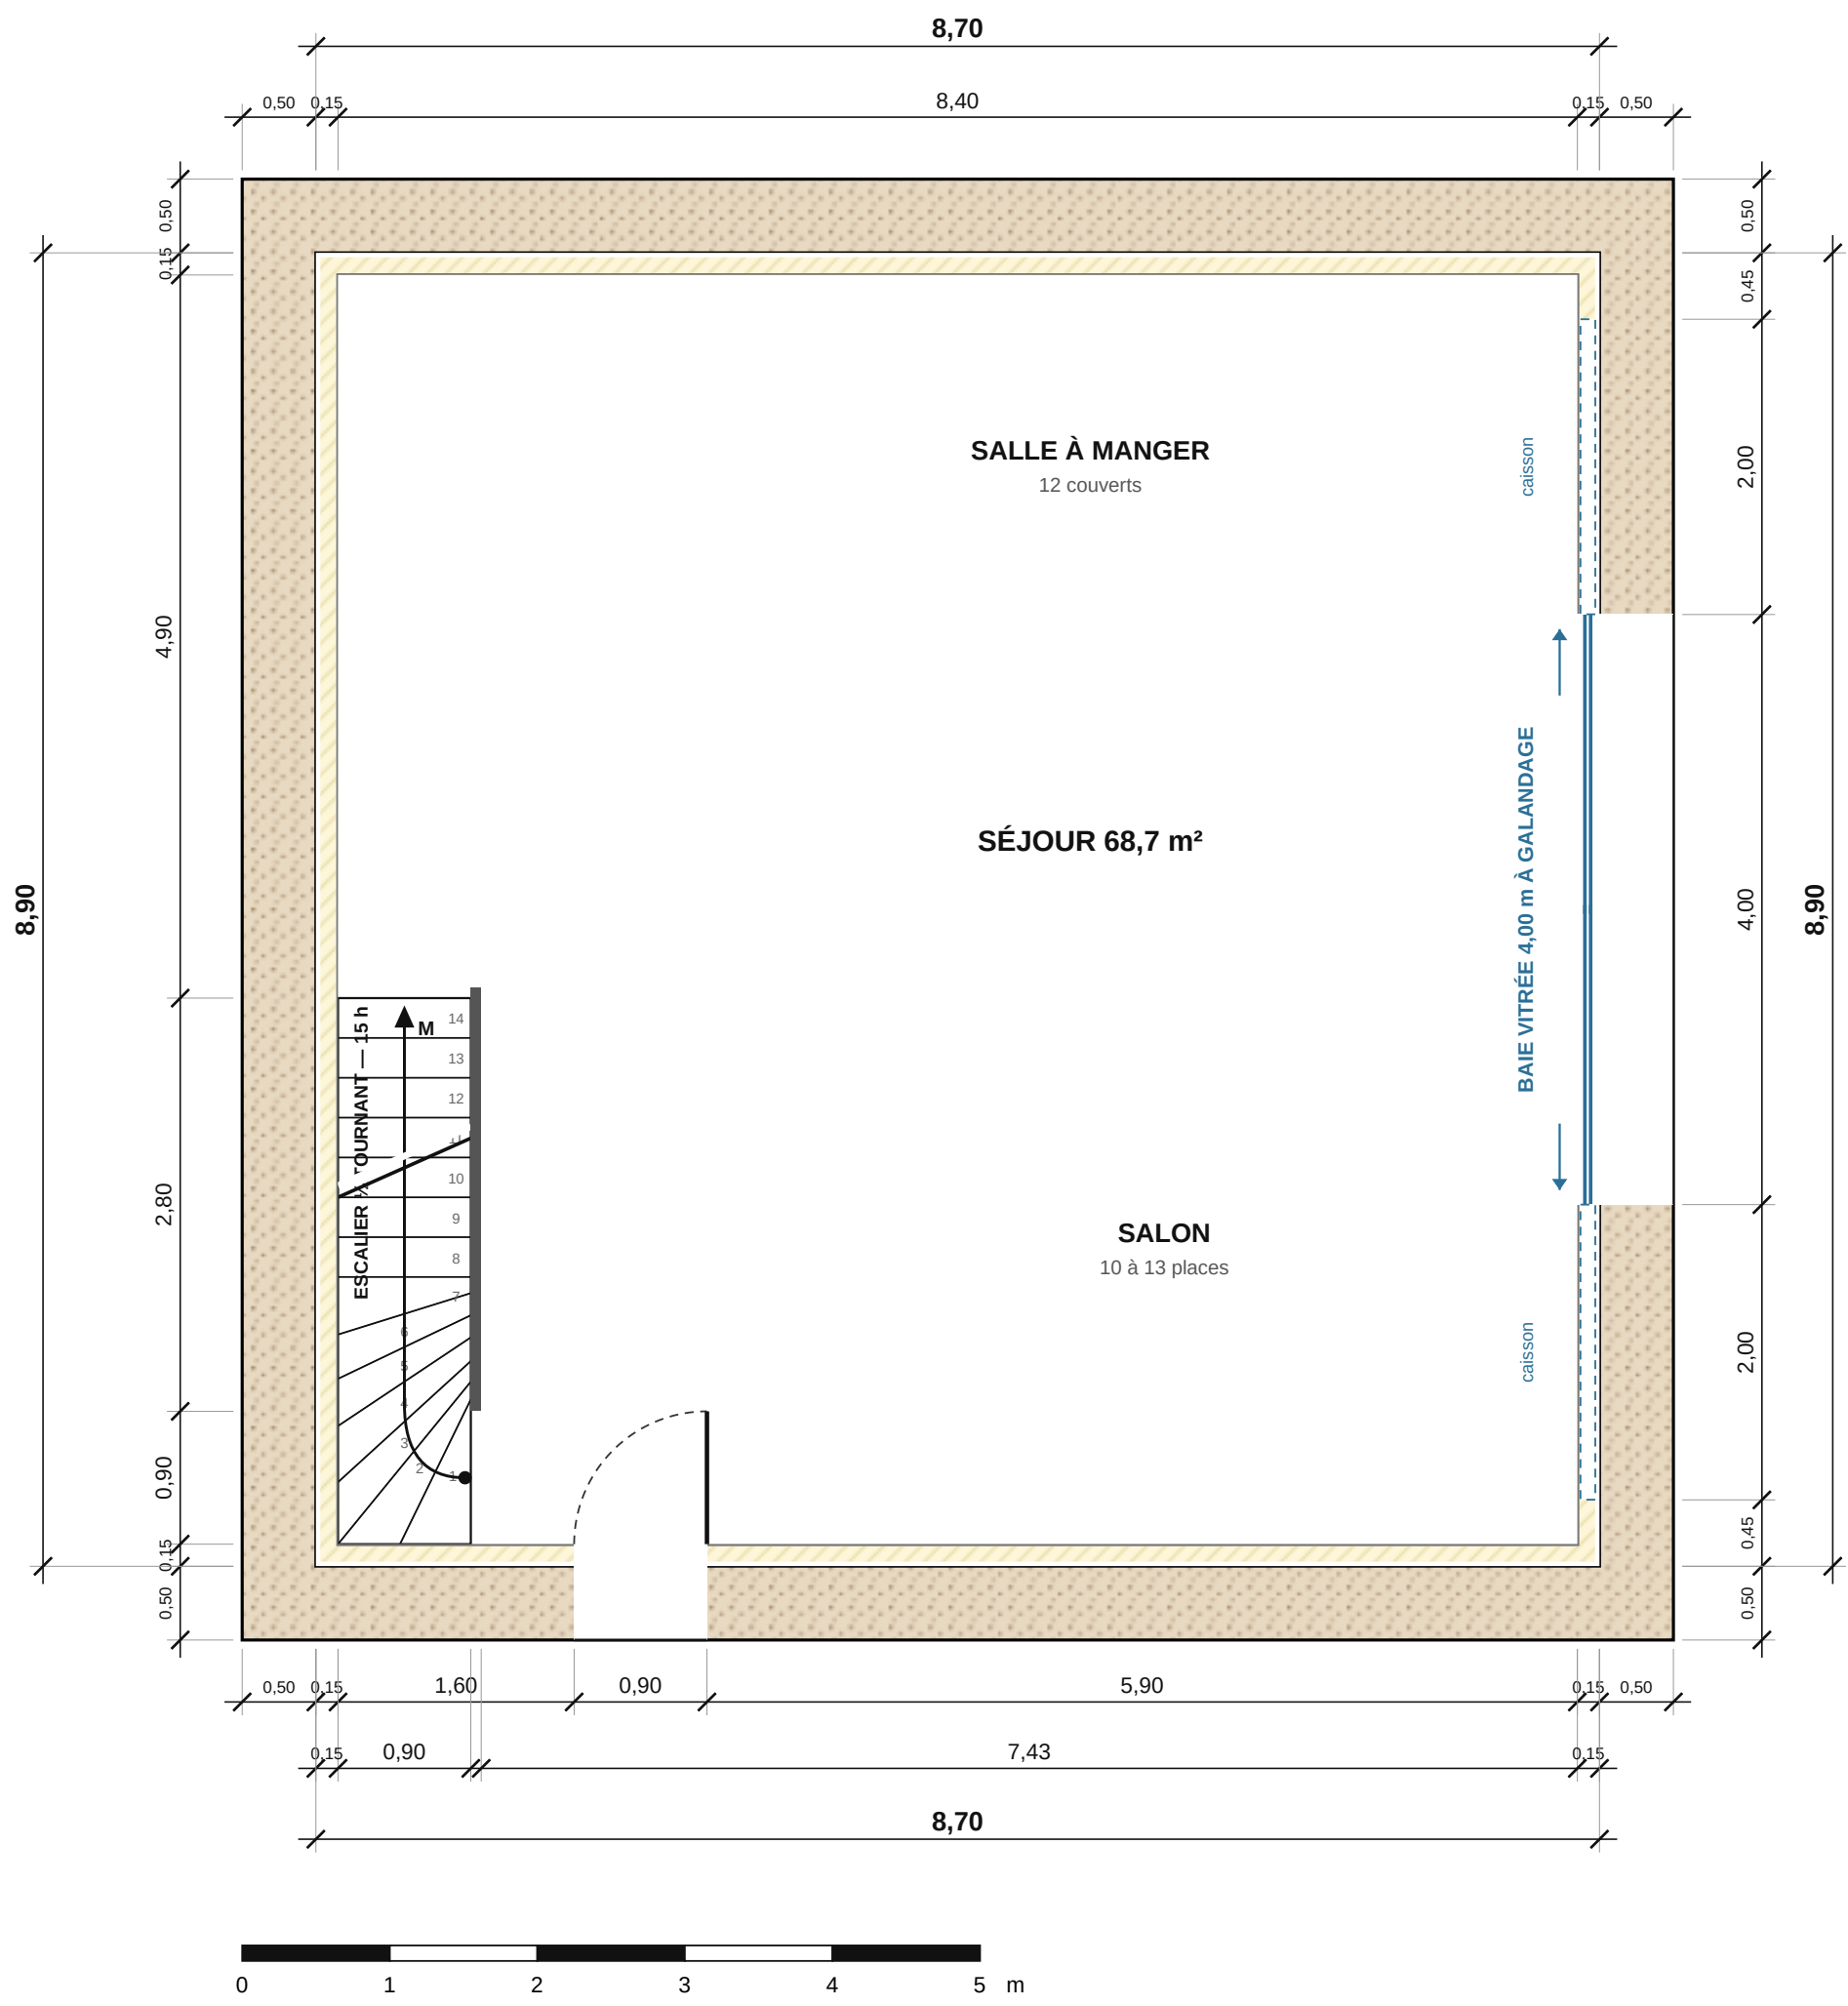


TABLEAU DES SURFACES

Séjour : salon + salle à manger	68,7 m²
Escalier (emprise)	3,3 m²
Total pièces (fini)	72,0 m²
Plateau murs nus 8,70 × 8,90 = 77,4 m²	
Intérieur fini (doublage 15) 8,40 × 8,60 = 72,2 m²	

NOTES

Murs pisé ≈ 50 cm + doublage 15 cm (lame d'air + isolant perspirant), comme à l'étage.
Baie vitrée 4,00 m à galandage, mur Est (jardin) : 2 vantaux de 2,00 m dans les murs.
Ouverture 4 m dans le pisé : linteau béton ou acier, étude BET obligatoire. Repli : 3,00 m.
Caissons : doublage épaissi local (≈ 20 cm).
Escalier identique à l'étage (¼ tournant bas).
Pièce unique : salon + salle à manger.
Salon en U ouvert sur la baie : canapés 3,60 + 3,20, 2 fauteuils, 2 poufs = 10 à 13 places.
Table 3,40 × 1,05 : 12 couverts (5 + 5 + 2).
Enfilade mur Nord, bibliothèque mur Ouest.
Accès Sud et autres ouvertures : à reporter selon l'existant.


Mur pisé existant	Doublage 15 (lame d'air)
Cloison neuve 7 cm	Baie vitrée galandage
Porte (P = passage)	Caisson galandage

PROJET
La Marinka — Rez-de-chaussée (77 m²)
Salon + salle à manger 12 pers. + baie jardin

PLAN RDC — PROJET COTÉ

ÉCHELLE 1/50 (A3)	DATE 04/10/2026	INDICE B — esquisse
-----------------------------	---------------------------	-------------------------------

PLAN RDC — AMÉNAGEMENT

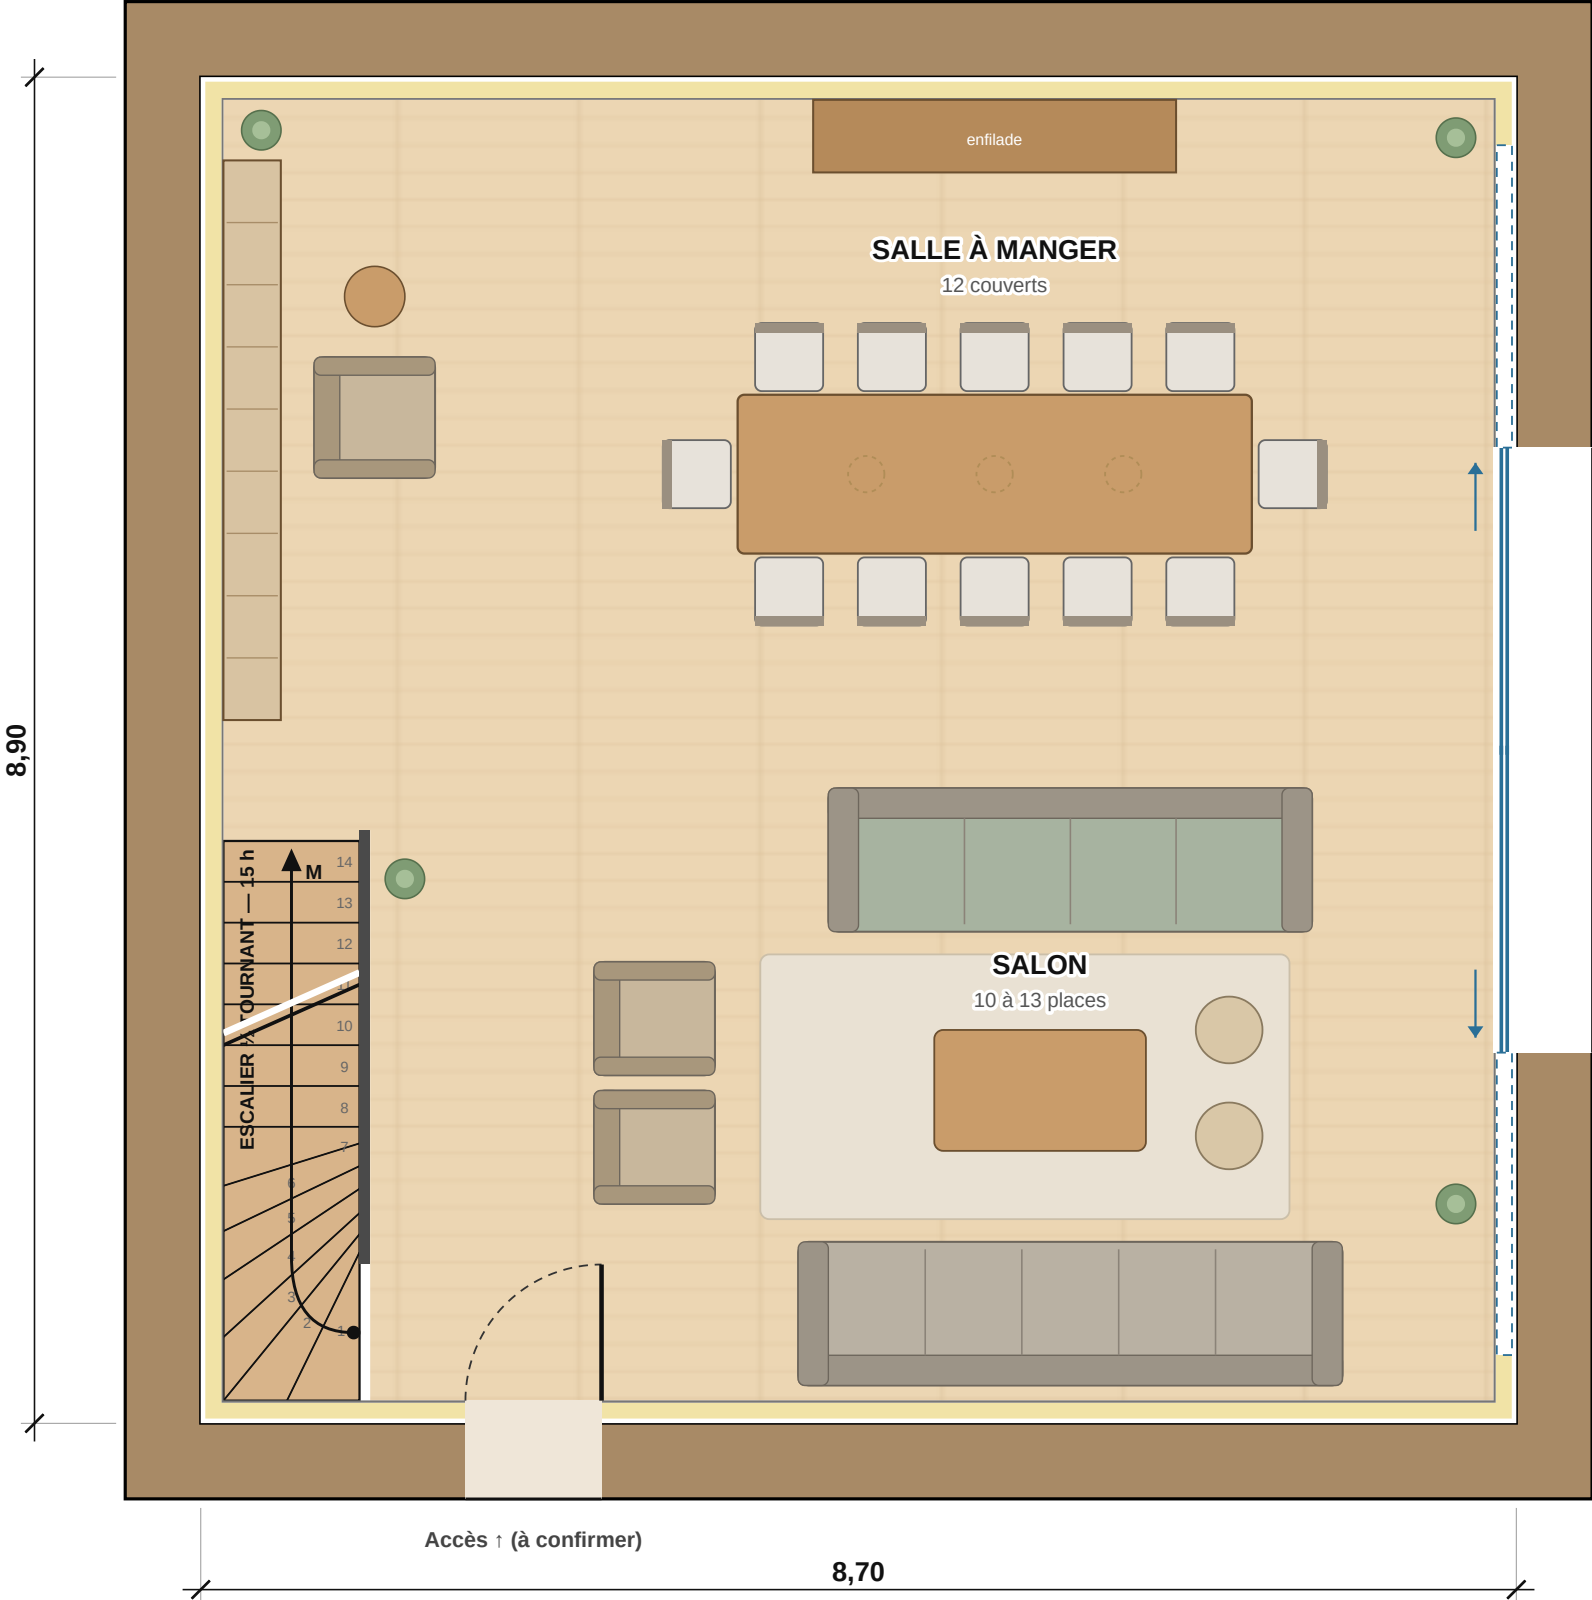

JARDIN

BAIE VITRÉE GALANDAGE 4,00 m — JARDIN

TABLEAU DES SURFACES

Séjour : salon + salle à manger	68,7 m²
Escalier (emprise)	3,3 m²
Total pièces (fini)	72,0 m²
Plateau murs nus 8,70 × 8,90 = 77,4 m²	
Intérieur fini (doublage 15) 8,40 × 8,60 = 72,2 m²	

NOTES

Murs pisé ≈ 50 cm + doublage 15 cm (lame d'air + isolant perspirant), comme à l'étage.
Baie vitrée 4,00 m à galandage, mur Est (jardin) : 2 vantaux de 2,00 m dans les murs.
Ouverture 4 m dans le pisé : linteau béton ou acier, étude BET obligatoire. Repli : 3,00 m.
Caissons : doublage épaissi local (≈ 20 cm).
Escalier identique à l'étage (¼ tournant bas).
Pièce unique : salon + salle à manger.
Salon en U ouvert sur la baie : canapés 3,60 + 3,20, 2 fauteuils, 2 poufs = 10 à 13 places.
Table 3,40 × 1,05 : 12 couverts (5 + 5 + 2).
Enfilade mur Nord, bibliothèque mur Ouest.
Accès Sud et autres ouvertures : à reporter selon l'existant.

Mur pisé existant	Doublage 15 (lame d'air)
Cloison neuve 7 cm	Baie vitrée galandage
Porte (P = passage)	Caisson galandage

PROJET
La Marinka — Rez-de-chaussée (77 m²)
Salon + salle à manger 12 pers. + baie jardin

PLAN RDC — AMÉNAGEMENT

ÉCHELLE 1/50 (A3)	DATE 04/10/2026	INDICE B — esquisse
-----------------------------	---------------------------	-------------------------------