

PLAN R+1 — PROJET COTÉ

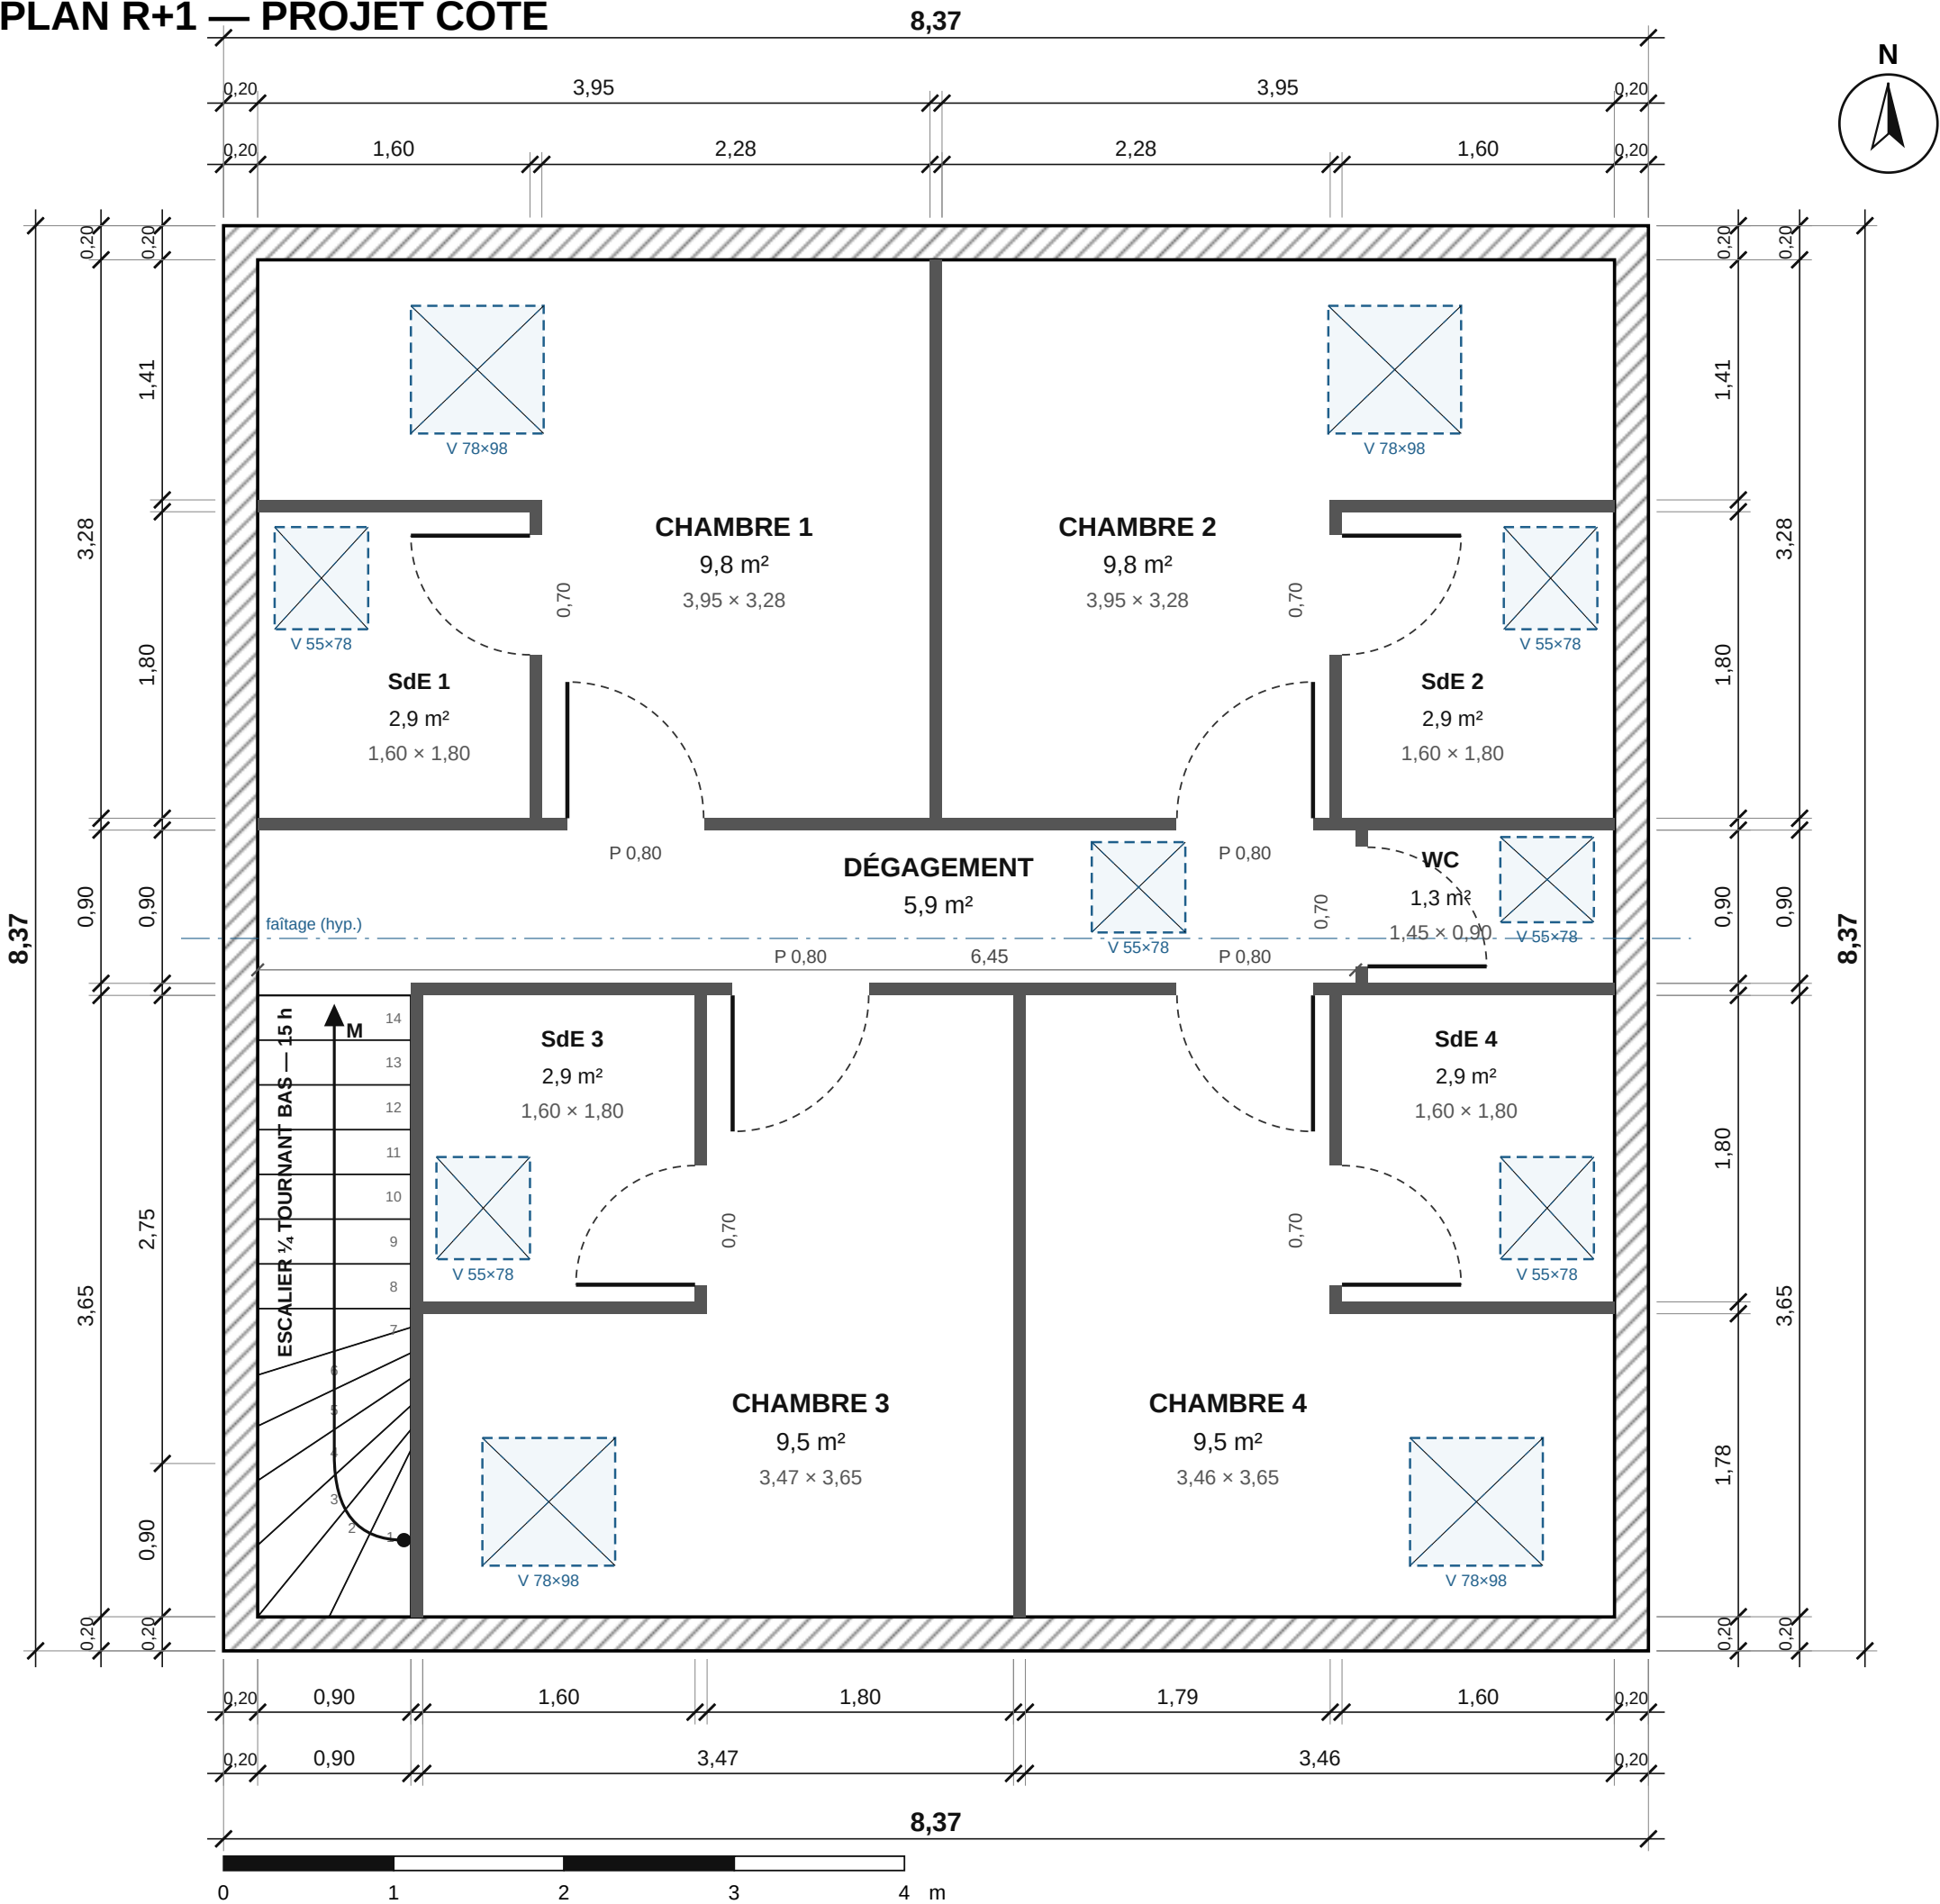


TABLEAU DES SURFACES

Chambre 1	9,8 m ²
Chambre 2	9,8 m ²
Chambre 3	9,5 m ²
Chambre 4	9,5 m ²
Salle d'eau 1	2,9 m ²
Salle d'eau 2	2,9 m ²
Salle d'eau 3	2,9 m ²
Salle d'eau 4	2,9 m ²
WC indépendant	1,3 m ²
Dégagement + palier	5,9 m ²
Trémie escalier	3,3 m ²

Total pièces 60,7 m²

Intérieur murs ext. 7,97 × 7,97 = 63,5 m²
Emprise 8,37 × 8,37 = 70 m²

NOTES

Murs ext. 20 cm — cloisons 7 cm (placo 72/48).
Cotes en mètres, intérieur brut de cloison.
Escalier ¼ tournant bas le long du mur Ouest :
départ côté Est le long du mur Sud, marches
balancées dans l'angle puis volée droite.
Emmarchement 0,90 — 15 hauteurs ≈ 19 cm
(à recaler sur la hauteur d'étage réelle).
Trémie 0,90 × 3,65 : avis structure / BET.
Éclairage uniquement par Velux (projection
en pointillés bleus). Faîtage E-O supposé.
Combles : zones sous 1,80 m hors Carrez,
à vérifier selon la hauteur sous rampant.
SdE : douche 90 × 120, vasque 80, VMC hygro.
WC suspendu + lave-mains, VMC.
Gaine Est : SdE 2 + WC + SdE 4 (chute Ø100).

Mur ext. conservé	Cloison neuve 7 cm
Velux (projection)	Porte (P = passage)

PROJET
Réaménagement de l'étage — 70 m²
4 chambres + 4 salles d'eau + WC indépendant

PLAN R+1 — PROJET COTÉ

ÉCHELLE 1/40 (A3)	DATE 04/10/2026	INDICE B — esquisse
----------------------	--------------------	------------------------

PLAN R+1 — AMÉNAGEMENT



TABLEAU DES SURFACES

Chambre 1	9,8 m²
Chambre 2	9,8 m²
Chambre 3	9,5 m²
Chambre 4	9,5 m²
Salle d'eau 1	2,9 m²
Salle d'eau 2	2,9 m²
Salle d'eau 3	2,9 m²
Salle d'eau 4	2,9 m²
WC indépendant	1,3 m²
Dégagement + palier	5,9 m²
Trémie escalier	3,3 m²

Total pièces 60,7 m²

Intérieur murs ext. 7,97 × 7,97 = 63,5 m²
Emprise 8,37 × 8,37 = 70 m²

NOTES

Murs ext. 20 cm — cloisons 7 cm (placo 72/48).
Cotes en mètres, intérieur brut de cloison.
Escalier ¼ tournant bas le long du mur Ouest :
départ côté Est le long du mur Sud, marches
balancées dans l'angle puis volée droite.
Emmarchement 0,90 — 15 hauteurs ≈ 19 cm
(à recaler sur la hauteur d'étage réelle).
Trémie 0,90 × 3,65 : avis structure / BET.
Éclairage uniquement par Velux (projection
en pointillés bleus). Faîtage E-O supposé.
Combles : zones sous 1,80 m hors Carrez,
à vérifier selon la hauteur sous rampant.
SdE : douche 90 × 120, vasque 80, VMC hygro.
WC suspendu + lave-mains, VMC.
Gaine Est : SdE 2 + WC + SdE 4 (chute Ø100).

Mur ext. conservé	Cloison neuve 7 cm
Velux (projection)	Porte (P = passage)

PROJET
Réaménagement de l'étage — 70 m²
4 chambres + 4 salles d'eau + WC indépendant

PLAN R+1 — AMÉNAGEMENT

ÉCHELLE 1/40 (A3)	DATE 04/10/2026	INDICE B — esquisse
----------------------	--------------------	------------------------